

arthea.

S T U D I O D E S I G N

@estudio.arthea

INDICE

- 01** PLANIMETRÍA DE ARQUITECTURA:
PLANTA, CORTE Y FACHADA
- 02** PLANIMETRÍA BASE DE INSTALACIÓN ELÉCTRICA:
PLANTEO DE INSTALACIÓN - PROPUESTA DE ILUMINARIA
- 03** PLANIMETRÍA BASE DE DESAGÜE PLUVIAL :
DETALLE RESOLUTIVO
- 04** PLANIMETRÍA DE PISOS Y REVESTIMIENTO DE PAREDES
- 05** MOBILIARIO
- 06** CARPINTERÍA - HERRERÍA
- 07** IDENTIDAD VISUAL
- 08** PLANIMETRÍA DE CARTELERIA - SEÑALETICA
- 09** RENDERS

01 PLANIMETRÍA DE ARQUITECTURA

PROYECTO:

LA PIAZZA!
LOCAL COMERCIAL


UBICACION:
RAWSON Y JUAN L. FANZOLATO
YERBA BUENA - TUCUMAN

CLIENTE:
MARCELO TORTI


TIPO DE PLANO:
PLANO DE ARQUITECTURA
PLANTA - FRENTE - CORTES

ESCALA:
1:75

OBSERVACIONES:
TODAS LAS MEDIDAS PROPORCIONADAS EN
PLANOS, DEBEN SER RECTIFICADAS EN
OBRA POR LA PERSONA RESPONSABLE A
EJECUTAR EL PROYECTO.

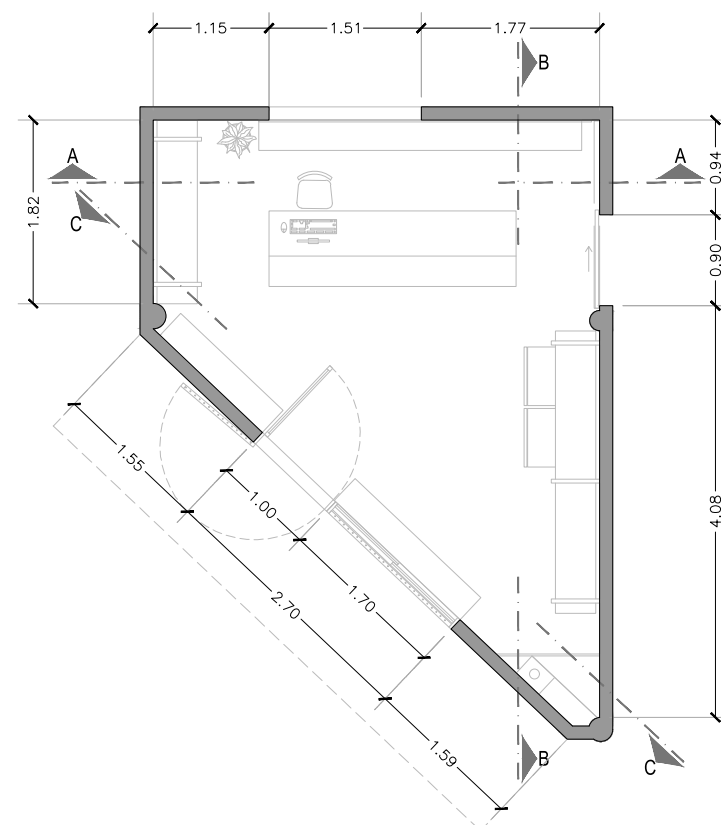


PLANTA ARQUITECTURA

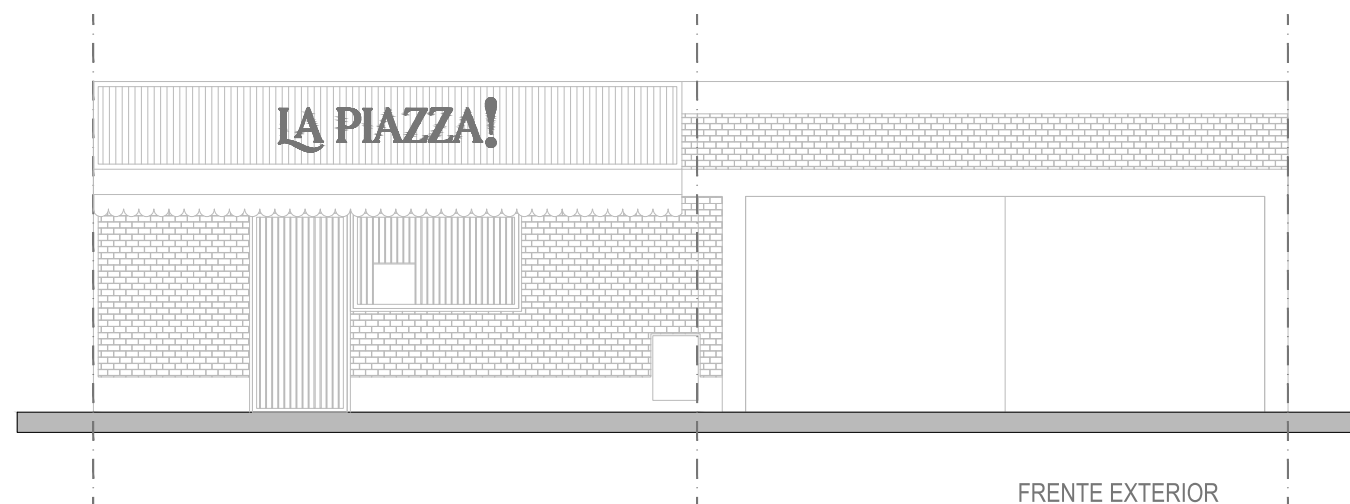


FRENTE EXTERIOR



CORTE A-A

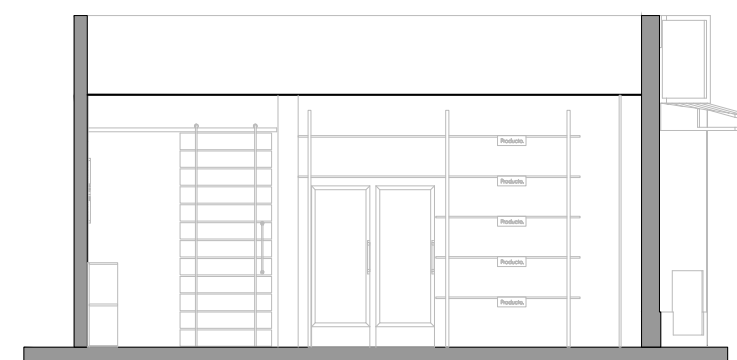

CORTE B-B

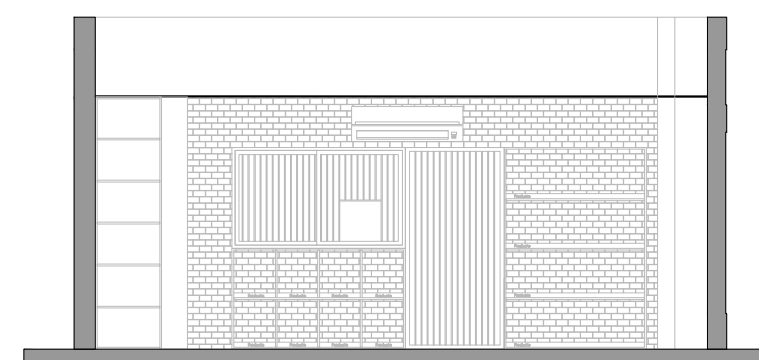

CORTE C-C

02 PLANIMETRÍA BASE DE INST. ELÉCTRICA

PROYECTO:

LA PIAZZA!
LOCAL COMERCIAL

UBICACION:
RAWSON Y JUAN L. FANZOLATO
YERBA BUENA - TUCUMAN

CLIENTE:
MARCELO TORTI

TIPO DE PLANO:
PLANO INST. ELÉCTRICA
PLANTEO - TABLA DE POTENCIA

ESCALA:
1:50

OBSERVACIONES:
TODAS LAS MEDIDAS PROPORCIONADAS EN
PLANOS, DEBEN SER RECTIFICADAS EN
OBRA POR LA PERSONA RESPONSABLE A
EJECUTAR EL PROYECTO.

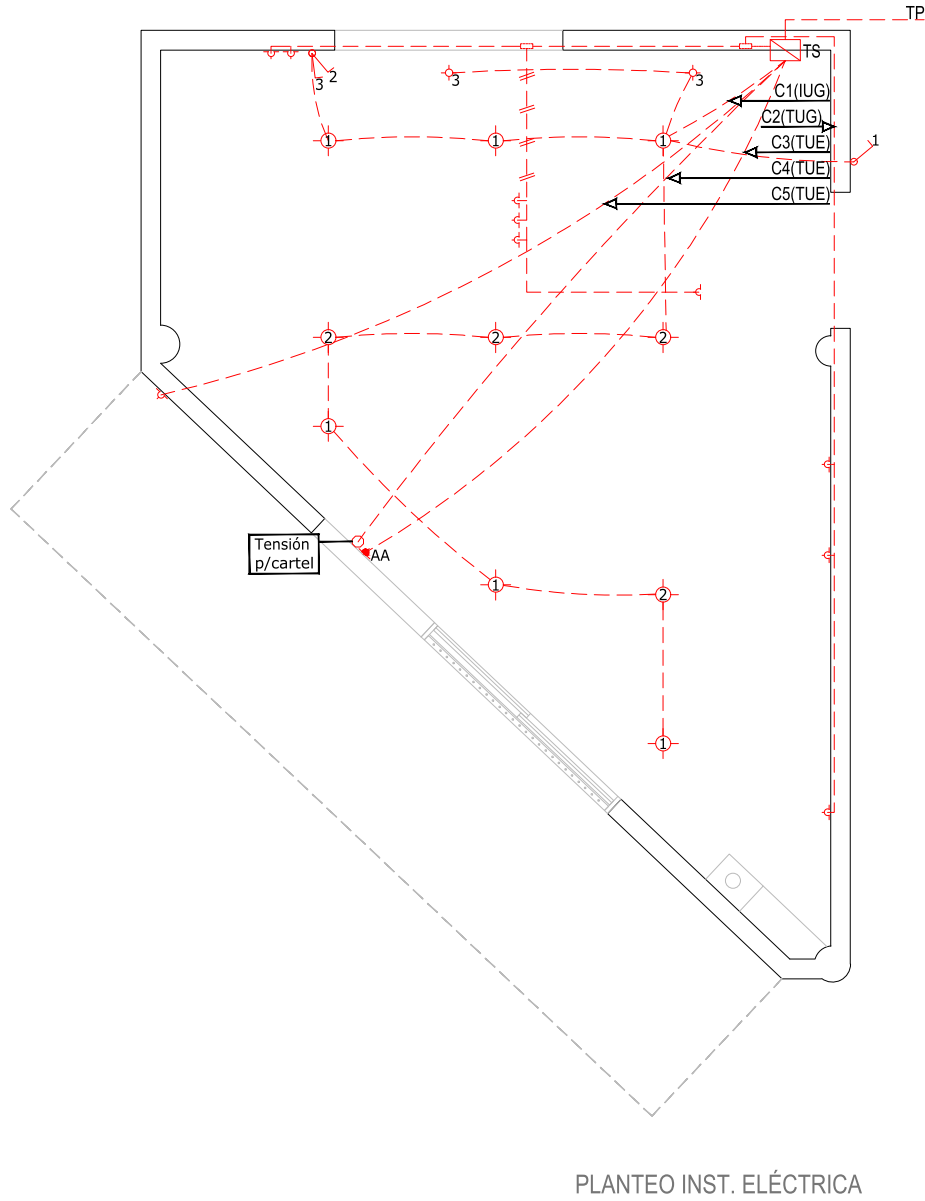


TABLA DE POTENCIA

MEDIDOR	CIRCUITO		TABLERO	UBICACION PLANTAS	BOCAS		MOTORES	TENSION	INTENSIDAD	POTENCIA
	Nº	TIPO			ILUM.	TOMA		VOLT (V)	AMP (A)	VATIO (W)
LOCAL COMERCIAL	C1	IUG Ilum. uso grai	TS	PB	12			220	10	120
	C2	TUG Tomas. uso grai	TS	PB		9		220	16	900
	C3	TUE Toma uso especial	TS	PB		1		220	20	1100
	C4	TUE Toma uso especial	TS	PB		1		220	20	1100
	C5	TUE Toma uso exterior	TS	PB		1		220	16	100
	5	TOTAL			12	12				3320

Este diagrama detalla la instalación eléctrica para el restaurante 'El Pajarito'. Muestra la distribución de los circuitos, las cargas y los puntos de conexión. Las cargas están representadas por iconos: un círculo con una 'X' para iluminación (10 unidades), un triángulo para tomacorrientes (10 unidades), un rectángulo para un tomacorriente especial (1 unidad), y un símbolo de motor para el ventilador (1 unidad). Las líneas de color rojo indican los recorridos de los cables, con números que representan la longitud en metros: 1, 2, 3, 4 y 5. Las etiquetas indican las alturas de las instalaciones: h:0.40m, h:1.23m, h:2.20m, h:2.80m y h:1.15m. Se especifica la tensión de 120V y se menciona la presencia de un tomacorriente para heladeras y un tomacorriente para el cartel. El diagrama también muestra la ubicación de la toma exterior y la toma para el ventilador.

PROPUESTA DE LUMINARIA

SPOT AR 111 SIMPLE
DE EMBUTIR



APLIQUE BARRAL
4 LUCES DIRECCIONALES - 120 CM DE LARGO



APLIQUE BARRAL
6 LUCES DIRECCIONALES - 120 CM DE LARGO



SPOT DICROICAS
DE EMBUTIR



TIRA LED



FICHA TÉCNICA

CANTIDAD: 06 unidades
UBICACIÓN: distribuidos en la superficie total
TIPO DE LUZ: cálida

Se corroborará in situ la ubicación en referencia al plano de ubicación provisto pero abierto a ajustes en obra.

FICHA TÉCNICA

CANTIDAD: 01 unidades
UBICACIÓN: distribuidos en la superficie total
TIPO DE LUZ: cálida

Se corroborará in situ la ubicación en referencia al plano de ubicación provisto pero abierto a ajustes en obra.

FICHA TÉCNICA

CANTIDAD: 03 unidades
UBICACIÓN: distribuidos en la superficie total
TIPO DE LUZ: cálida

Se corroborará in situ la ubicación en referencia al plano de ubicación provisto pero abierto a ajustes en obra.

FICHA TÉCNICA

CANTIDAD: 02 unidades
UBICACIÓN: sobre el mueble detrás del mostrador
TIPO DE LUZ: cálida

Se corroborará in situ la ubicación en referencia al plano de ubicación provisto pero abierto a ajustes en obra.

FICHA TÉCNICA

CANTIDAD: 1 unidad
UBICACIÓN: en mostrador
TIPO DE LUZ: cálida

Se corroborará in situ la ubicación en referencia al plano de ubicación provisto pero abierto a ajustes en obra.

03 PLANIMETRÍA BASE DE DESAGÜE PLUVIAL

PROYECTO:

LA PIAZZA!
LOCAL COMERCIAL


UBICACION:
RAWSON Y JUAN L. FANZOLATO
YERBA BUENA - TUCUMAN

CLIENTE:
MARCELO TORTI



TIPO DE PLANO:
PLANO DESAGÜE PLUVIAL
PLANTA - DETALLE 3D

ESCALA:
1:50

OBSERVACIONES:
TODAS LAS MEDIDAS PROPORCIONADAS EN
PLANOS, DEBEN SER RECTIFICADAS EN
OBRA POR LA PERSONA RESPONSABLE A
EJECUTAR EL PROYECTO.

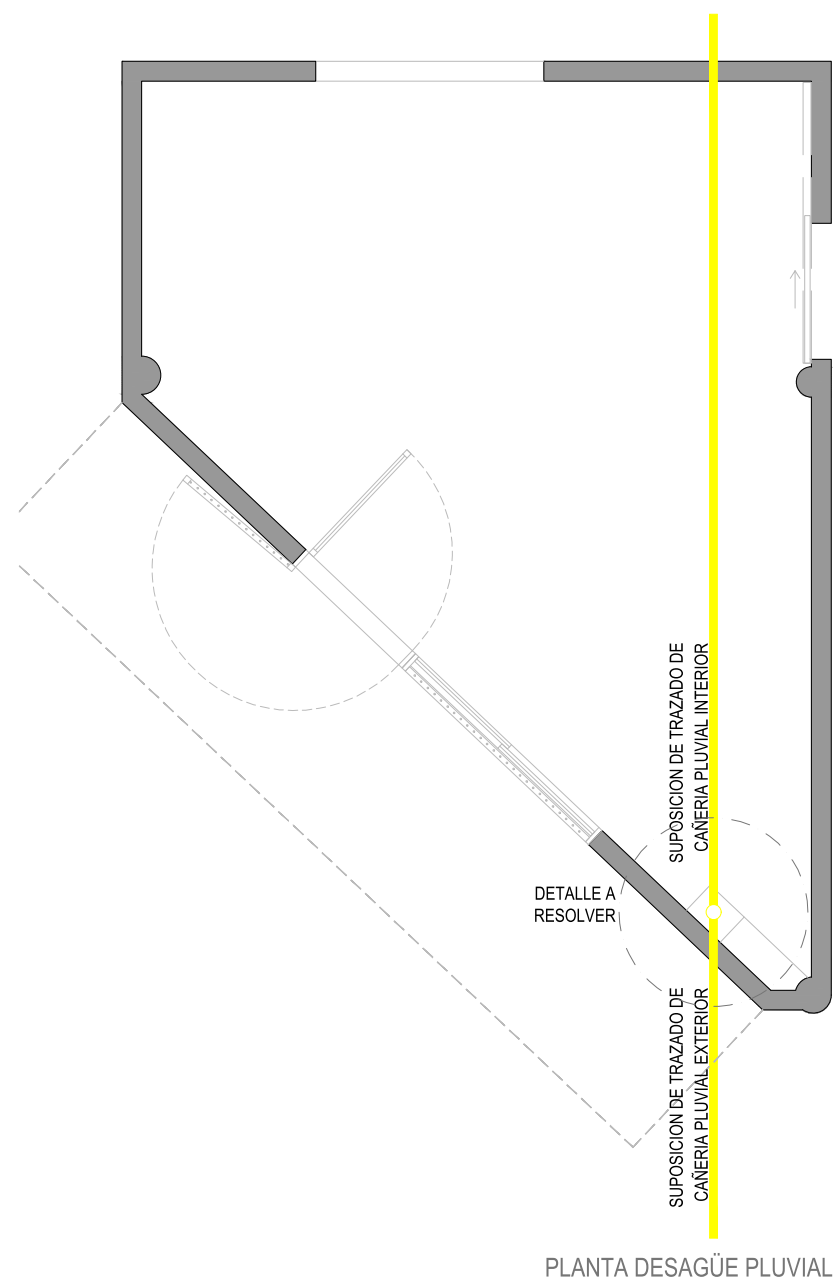

DETALLE VINCULACIÓN DE CAÑERÍAS

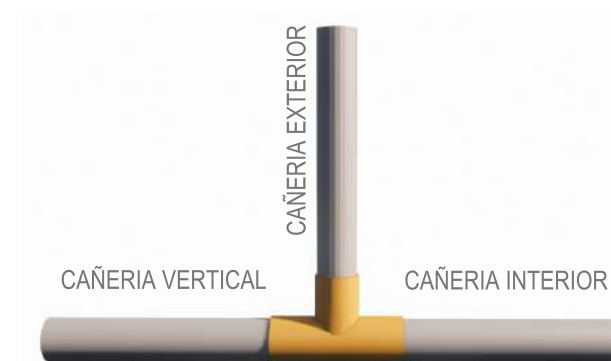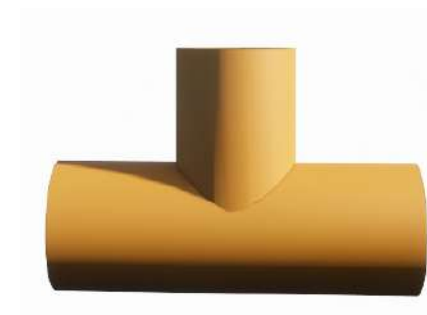

SE PROPONE LA RESOLUCION DEL ENCUENTRO DE CAÑERIA INTERIOR, VERTICAL Y EXTERIOR DE DESAGUE PLUVIAL, MEDIANTE LA PIEZA DE VINCULACION "T".
SE DEBERA CONSULTAR CON UN PLOMERO ANTES DE EJECUTAR EL MISMO.

04 PLANIMETRÍA DE PISOS Y REVESTIMIENTO EN PAREDES

PROYECTO:

LA PIAZZA!
LOCAL COMERCIAL


UBICACION:
RAWSON Y JUAN L. FANZOLATO
YERBA BUENA - TUCUMAN

CLIENTE:
MARCELO TORTI

TIPO DE PLANO:
PLANIMETRIA DE PISOS Y
RESVESTIMIENTOS
PLANTA - IMAGEN REPRESENTATIVA

ESCALA:
1:50

OBSERVACIONES:
TODAS LAS MEDIDAS PROPORCIONADAS EN
PLANOS, DEBEN SER RECTIFICADAS EN
OBRA POR LA PERSONA RESPONSABLE A
EJECUTAR EL PROYECTO.

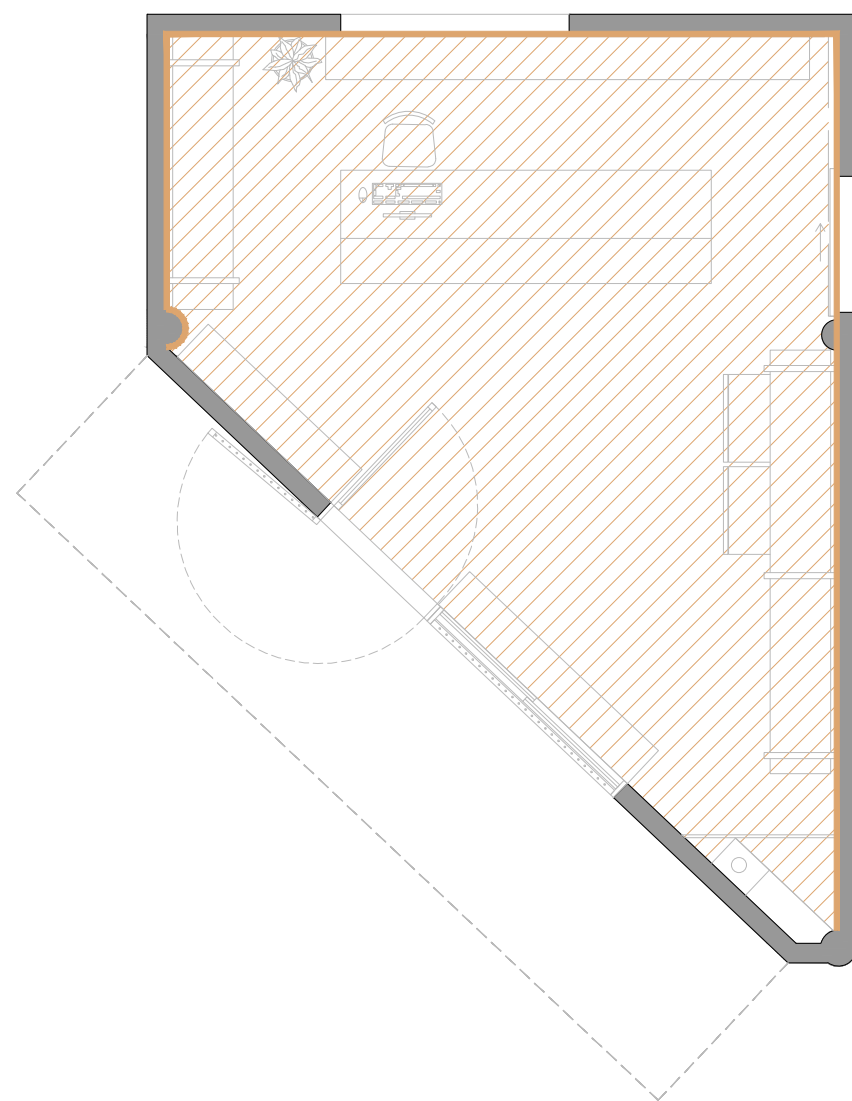

PLANTA DE REVESTIMIENTO

 **PISO** - microcemento
tono: blanco nieve
marca: EDFAN



 **PAREDES** - microcemento
tono: blanco nieve
marca: EDFAN



IMAGEN DE CATÁLOGO

05 MOBILIARIO

MOSTRADOR

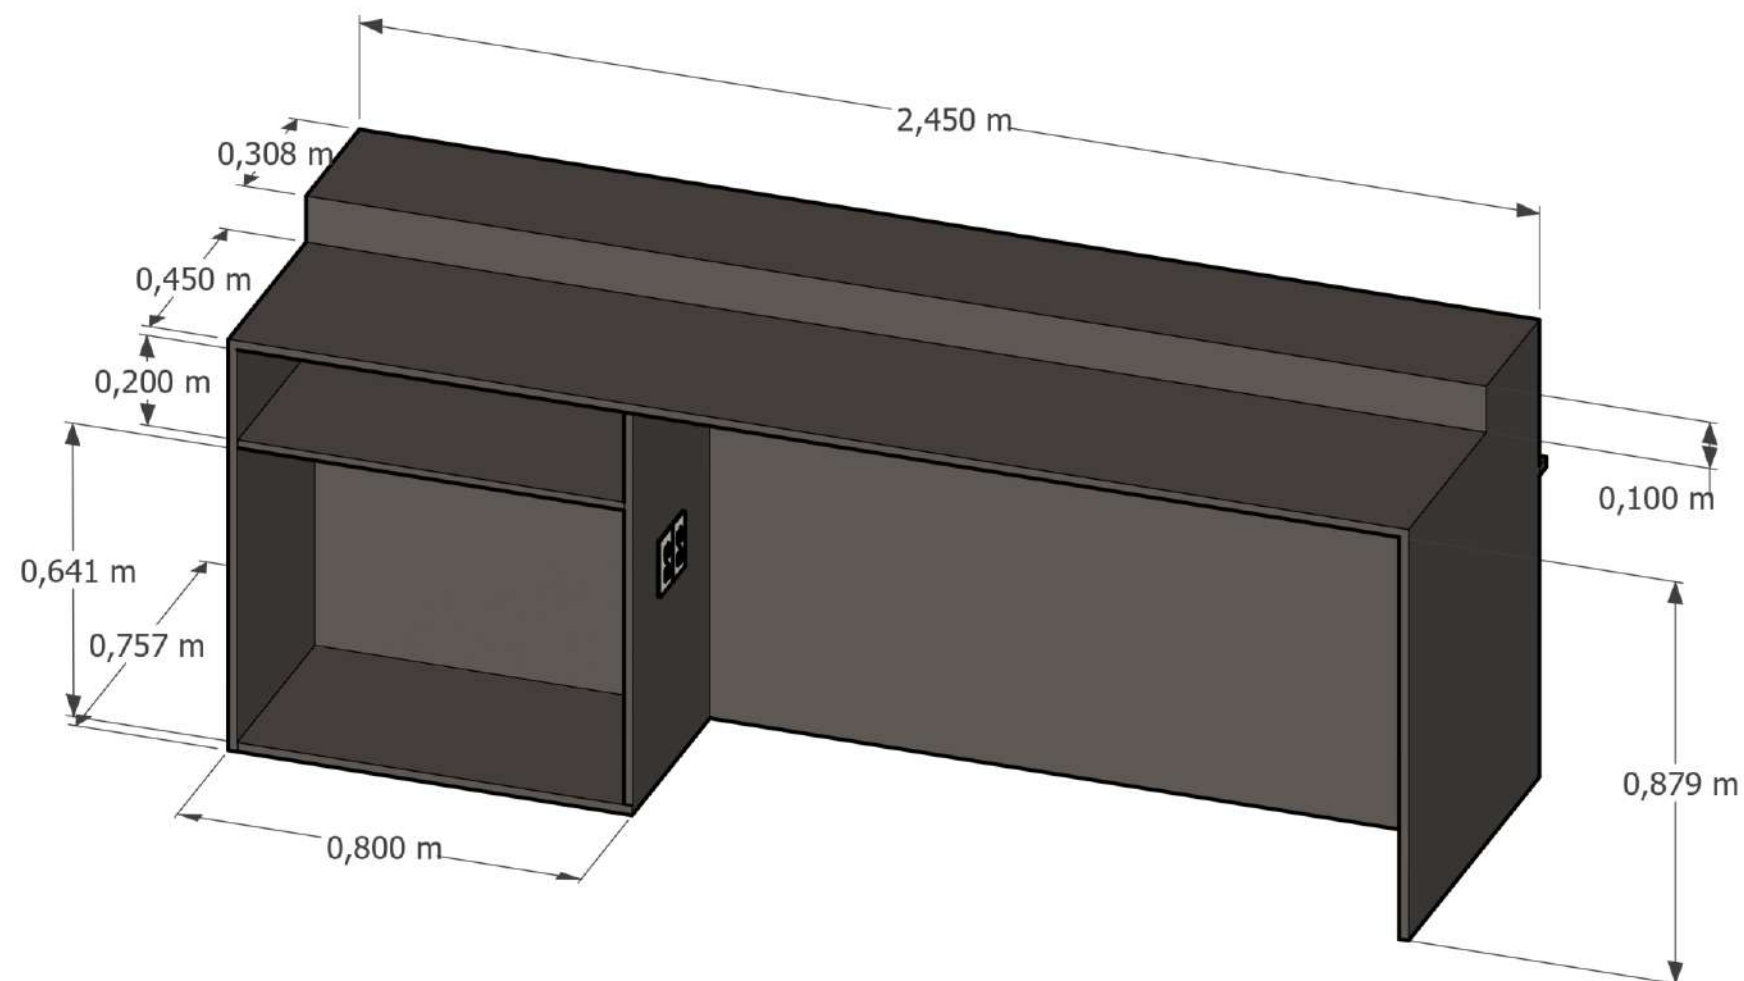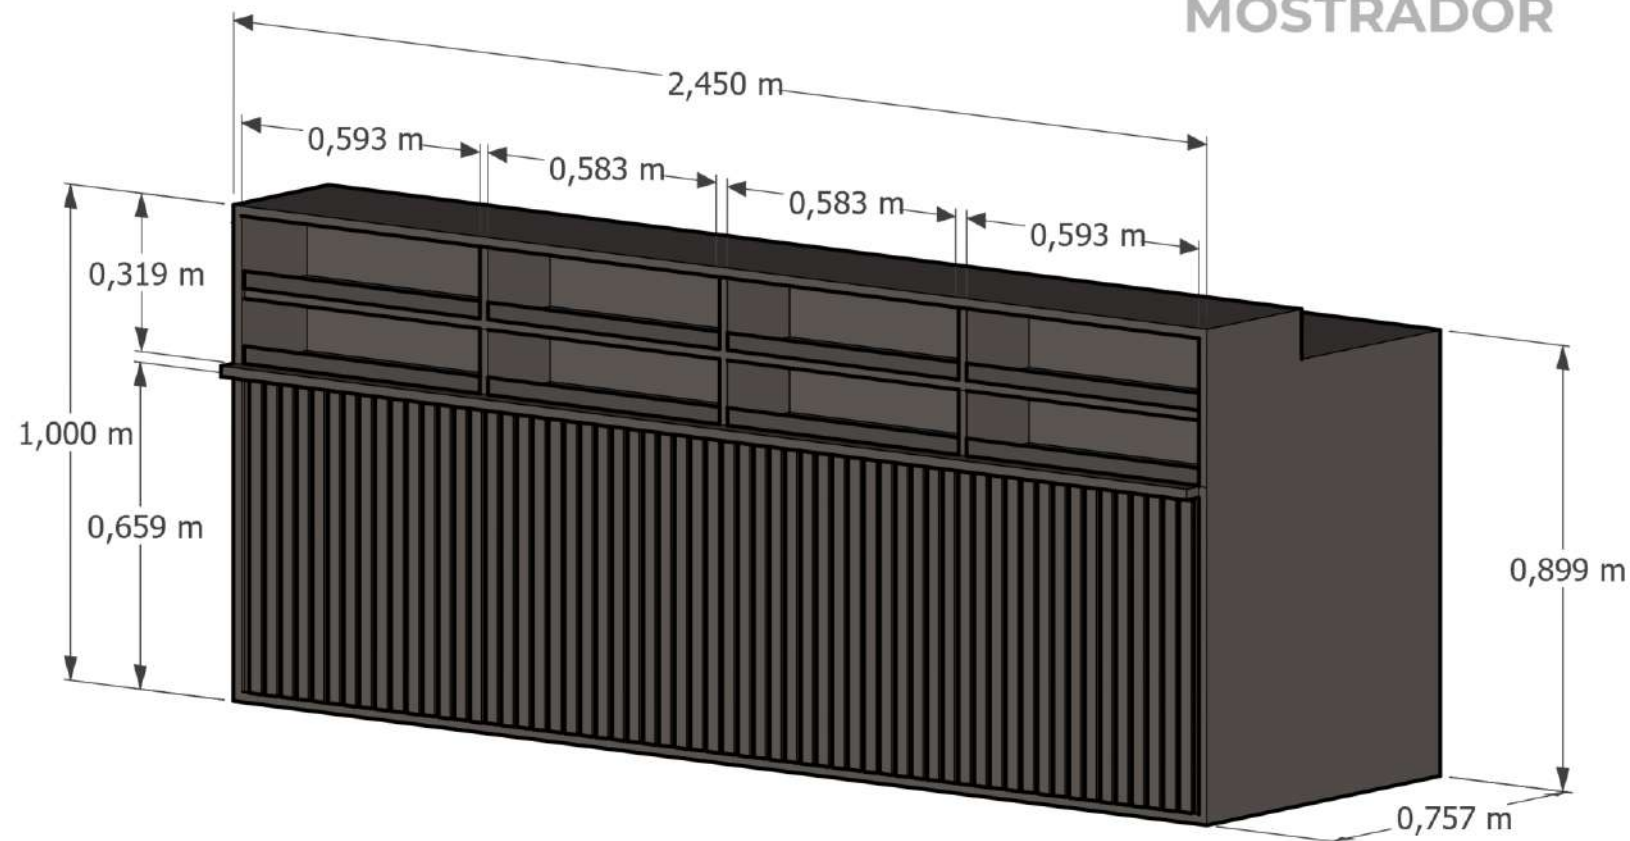

FICHA TÉCNICA

Descripción

Mueble funcional con diseño minimalista, destinado para exhibición de productos y atención al cliente, apoyo de sistema de cobro (computadora, caja registradora, etc). Incluye espacio de guardado y superficie de trabajo ergonómica para el operador.


Medidas generales

Sus dimensiones totales son 2,45 m largo x 0,75m profundidad x 1,00 m altura

Materiales

Melamina Faplac Tribal
Linea Étnica de 18mm


Panel de WPC Wud
Linea Nikko Grey

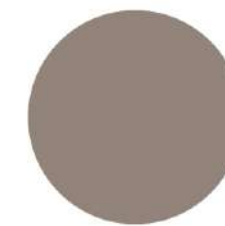

Observaciones

Verificar medidas en obra. Sujeto a confirmación final según el carpintero considere.

ESTANTERÍA

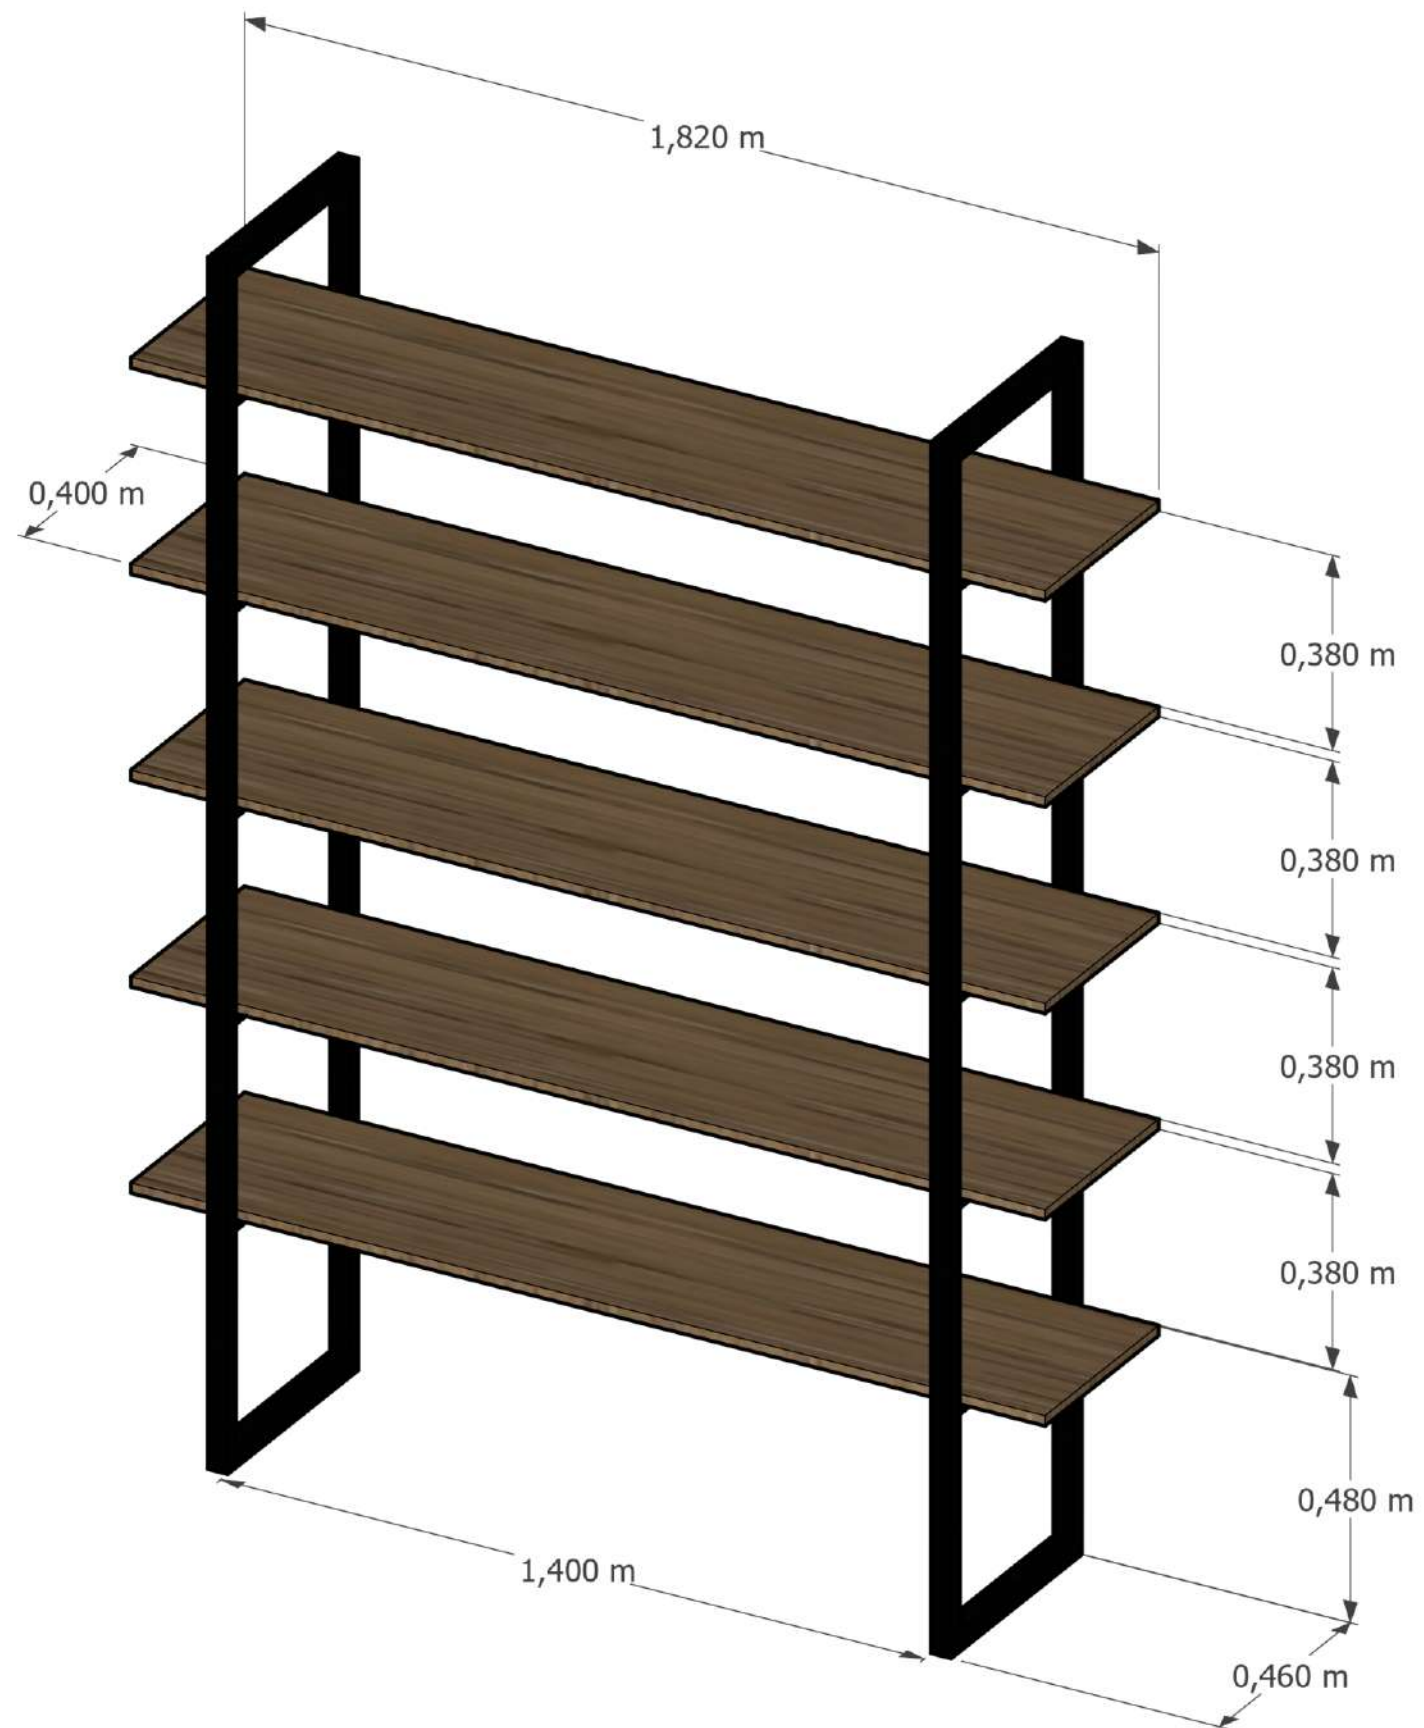

FICHA TÉCNICA

Descripción

Estante autoportante con estructuras de hierro para exhibición y almacenamiento de productos, de diseño industrial abierto que facilita reposición y limpieza. Estantes de melamina accesibles y bien espaciados apoyados directamente sobre estructura metálica.

Medidas generales

Sus dimensiones totales son 1,82 m largo x 0,46 m profundidad x 2,35 m altura

Materiales

Melamina Faplac
Carvalho Mezzo Linea
Nature de 18mm


Caño estructural de
hierro de 40 x 40 x 1,2
mm



Observaciones

Verificar medidas en obra. Sujeto a confirmación final según el carpintero/herrero considere.

ESTANTERÍA

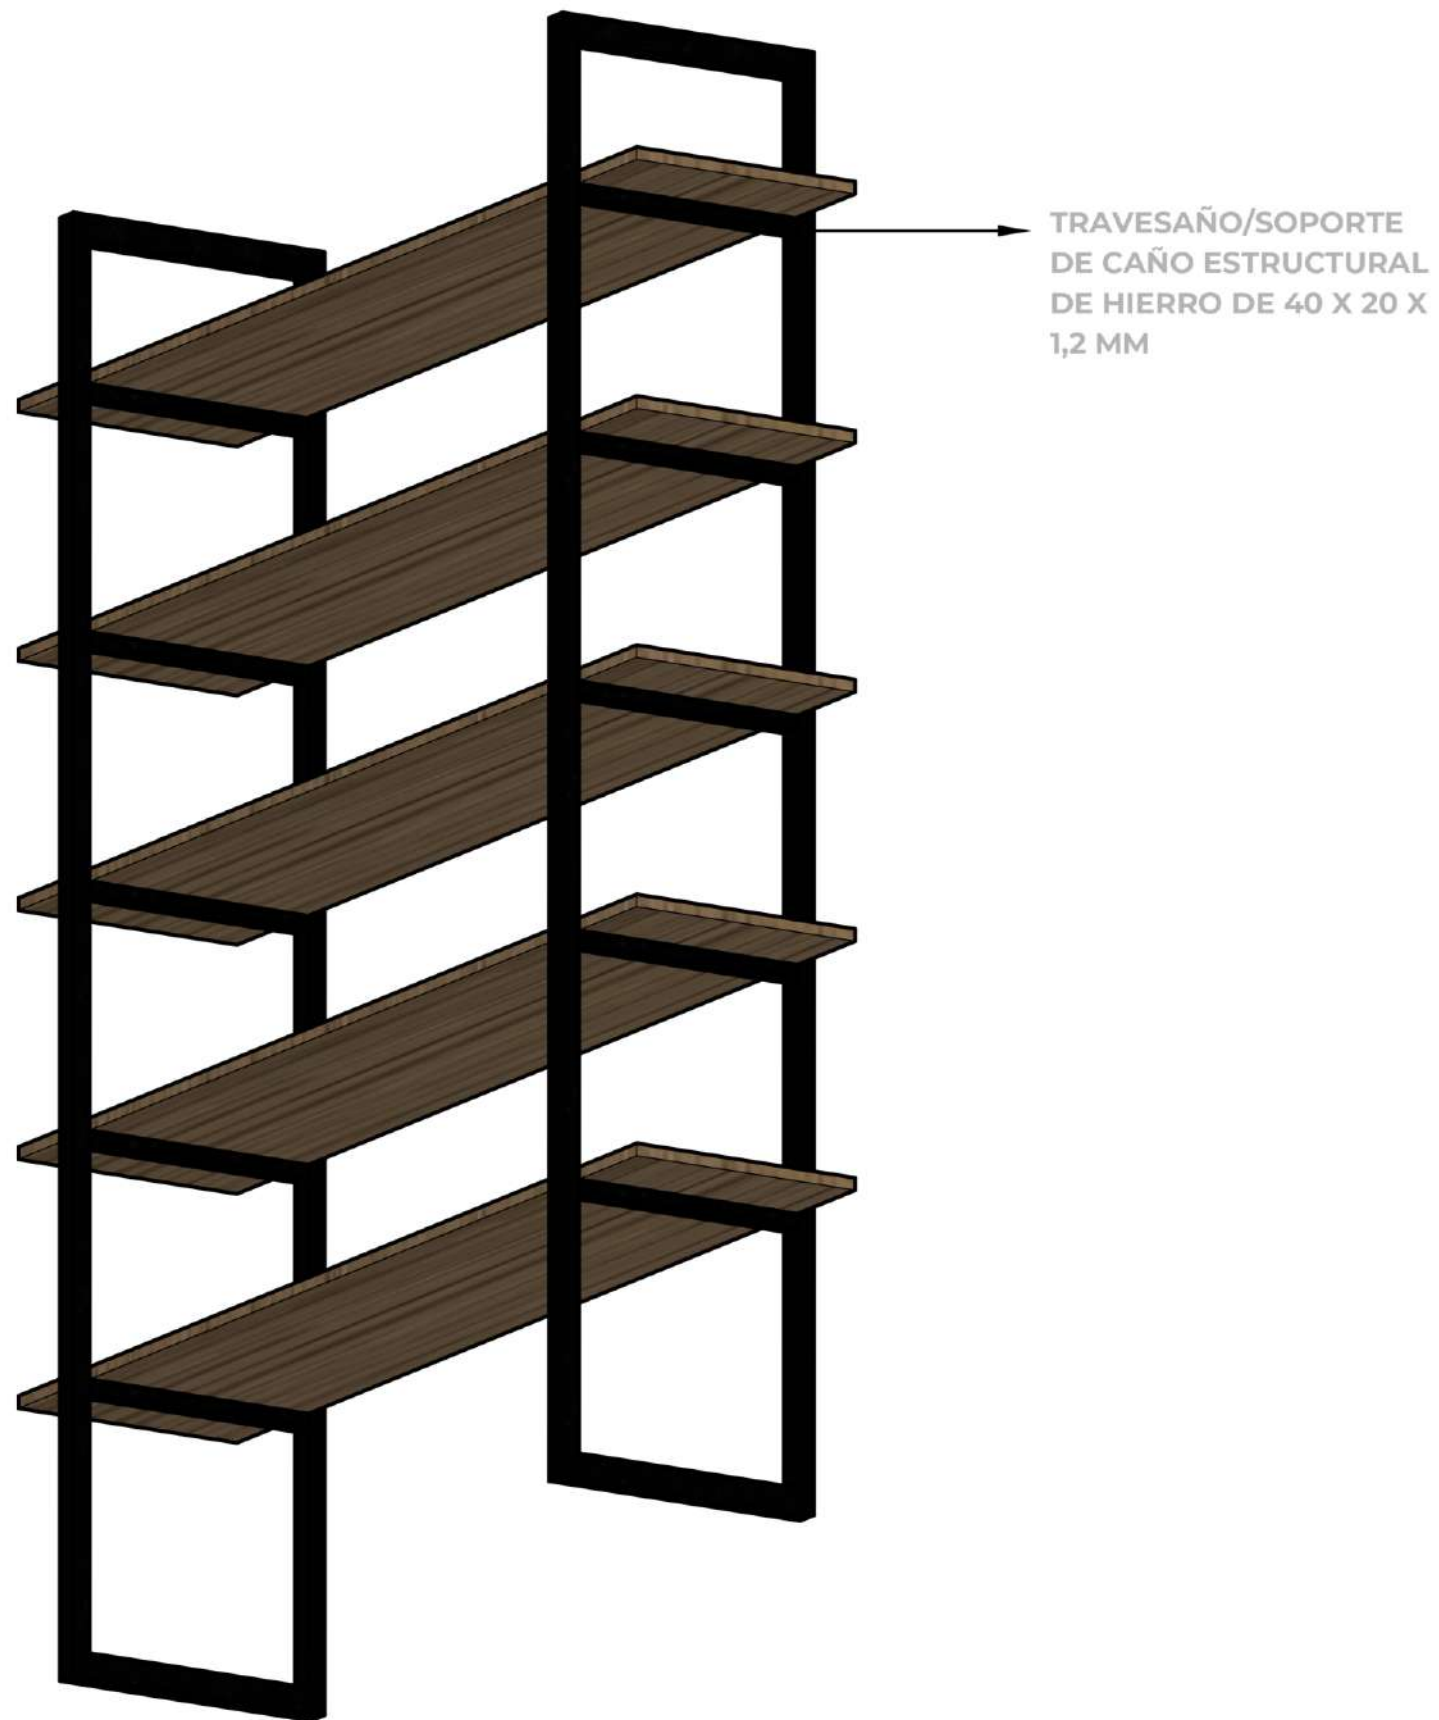

FICHA TÉCNICA

Descripción

Estante autoportante con estructuras de hierro para exhibición y almacenamiento de productos, de diseño industrial abierto que facilita reposición y limpieza. Estantes de melamina accesibles y bien espaciados apoyados directamente sobre estructura metálica.

Medidas generales

Sus dimensiones totales son 1,82 m largo x 0,46 m profundidad x 2,35 m altura

Materiales

Melamina Faplac
Carvalho Mezzo Linea
Nature de 18mm


Caño estructural de
hierro de 40 x 40 x 1,2
mm



Observaciones

Verificar medidas en obra. Sujeto a confirmación final según el carpintero/herrero considere.

ESTANTERÍA

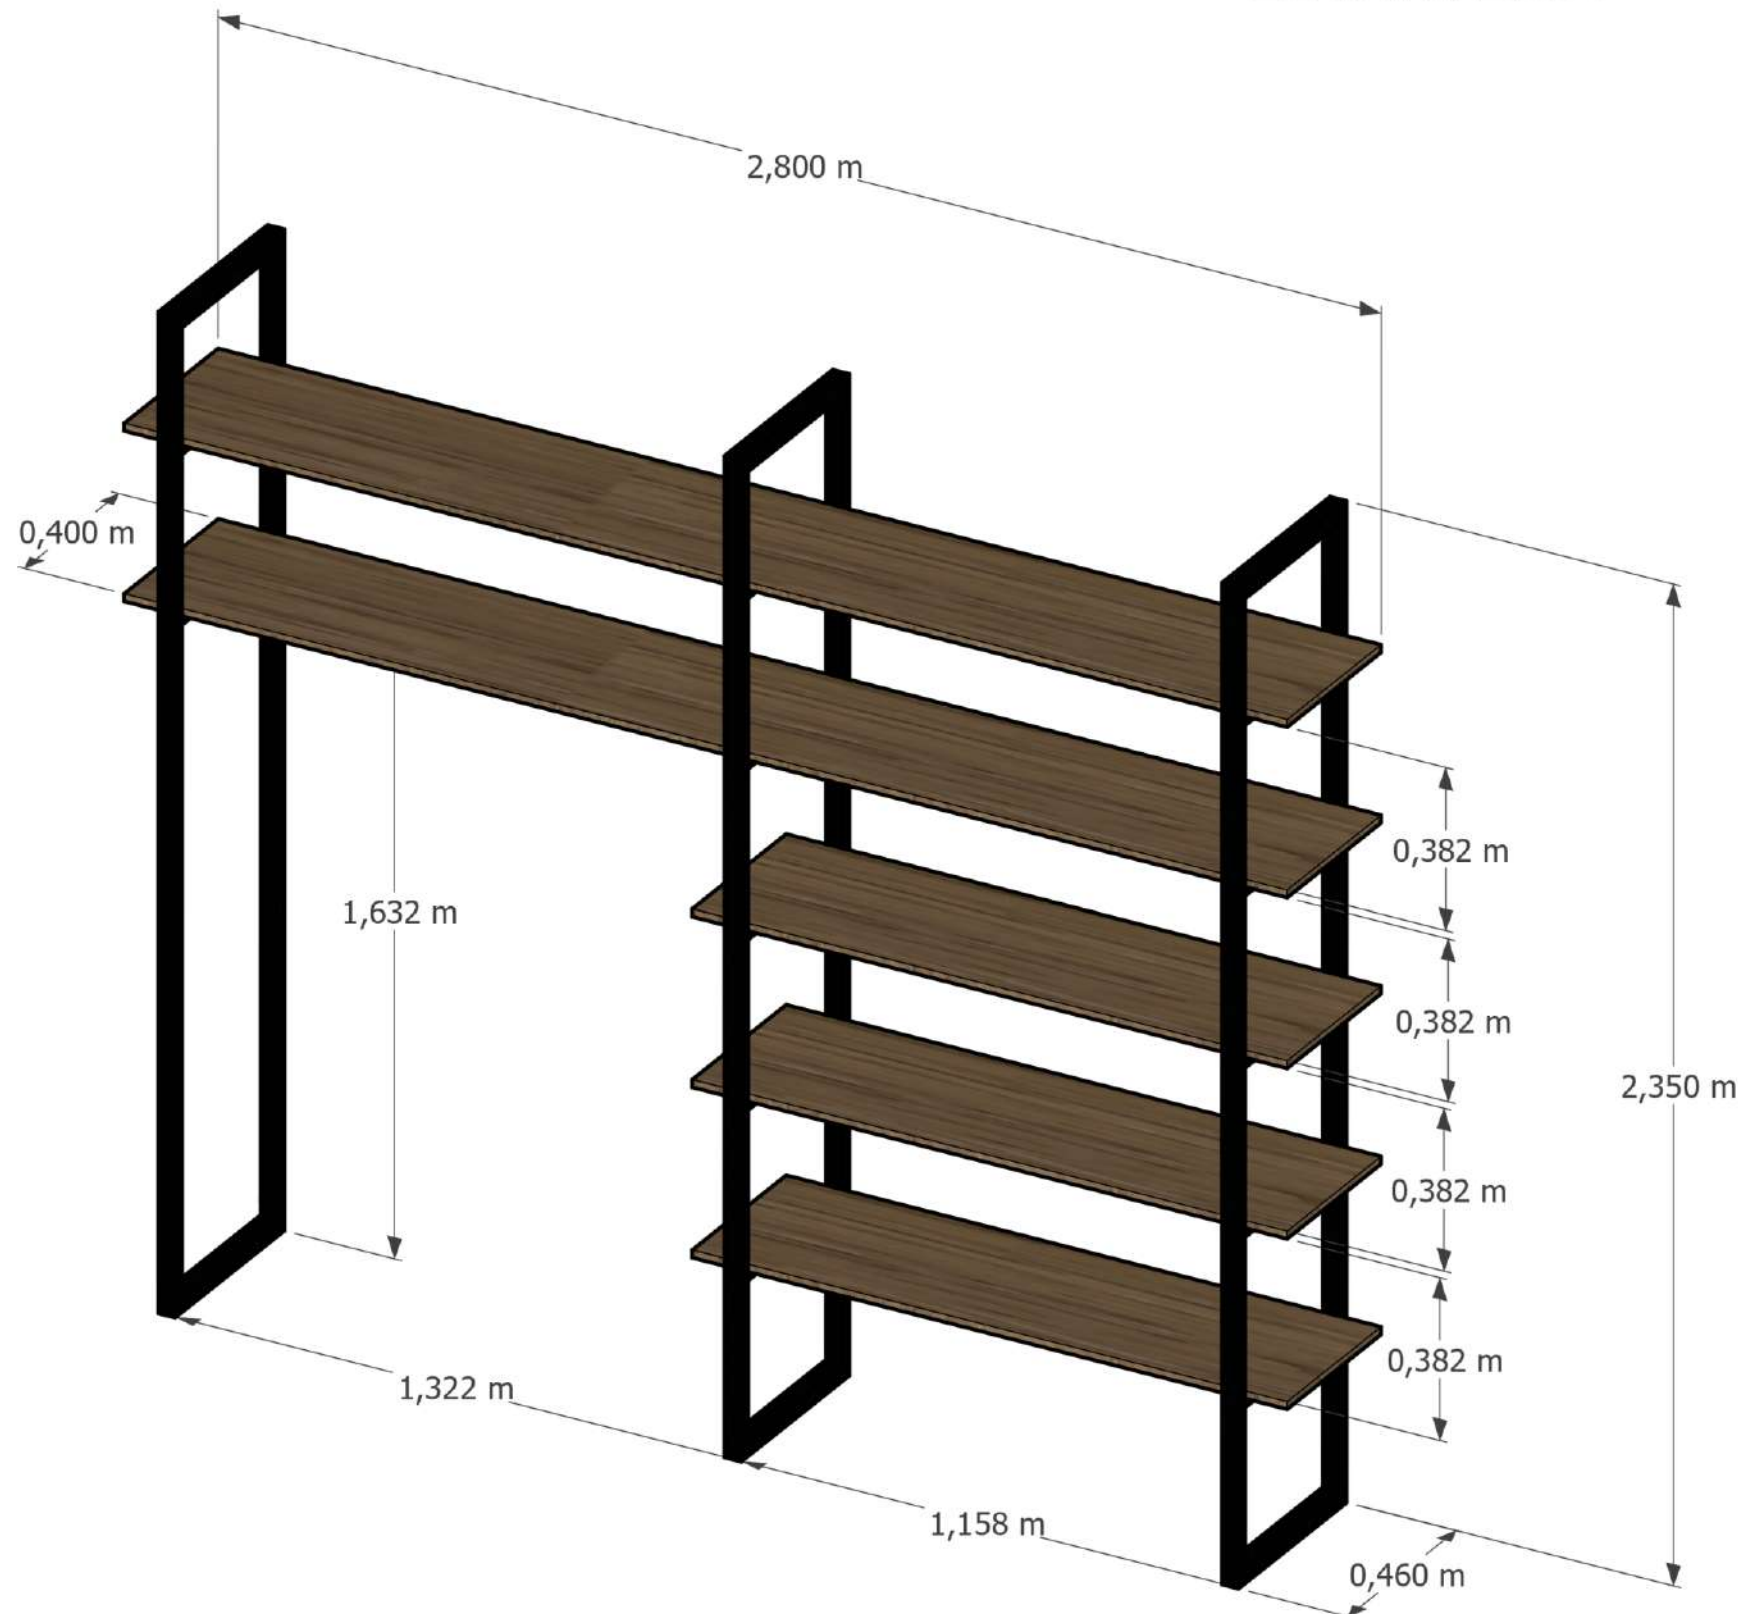

FICHA TÉCNICA

Descripción

Estante autoportante con estructuras de hierro para exhibición y almacenamiento de productos, de diseño industrial abierto que facilita reposición y limpieza. Con espacio cómodo de 1,63 m altura x 1,32 m largo para dos heladeras de exhibición de bebidas.

Medidas generales

Sus dimensiones totales son 2,80 m largo x 0,46 m profundidad x 2,35 m altura

Materiales

Melamina Faplac
Carvalho Mezzo Linea
Nature de 18mm


Caño estructural de
hierro de 40 x 40 x 1,2
mm



Observaciones

Verificar medidas en obra. Sujeto a confirmación final según el carpintero/herrero considere.

ESTANTERÍA

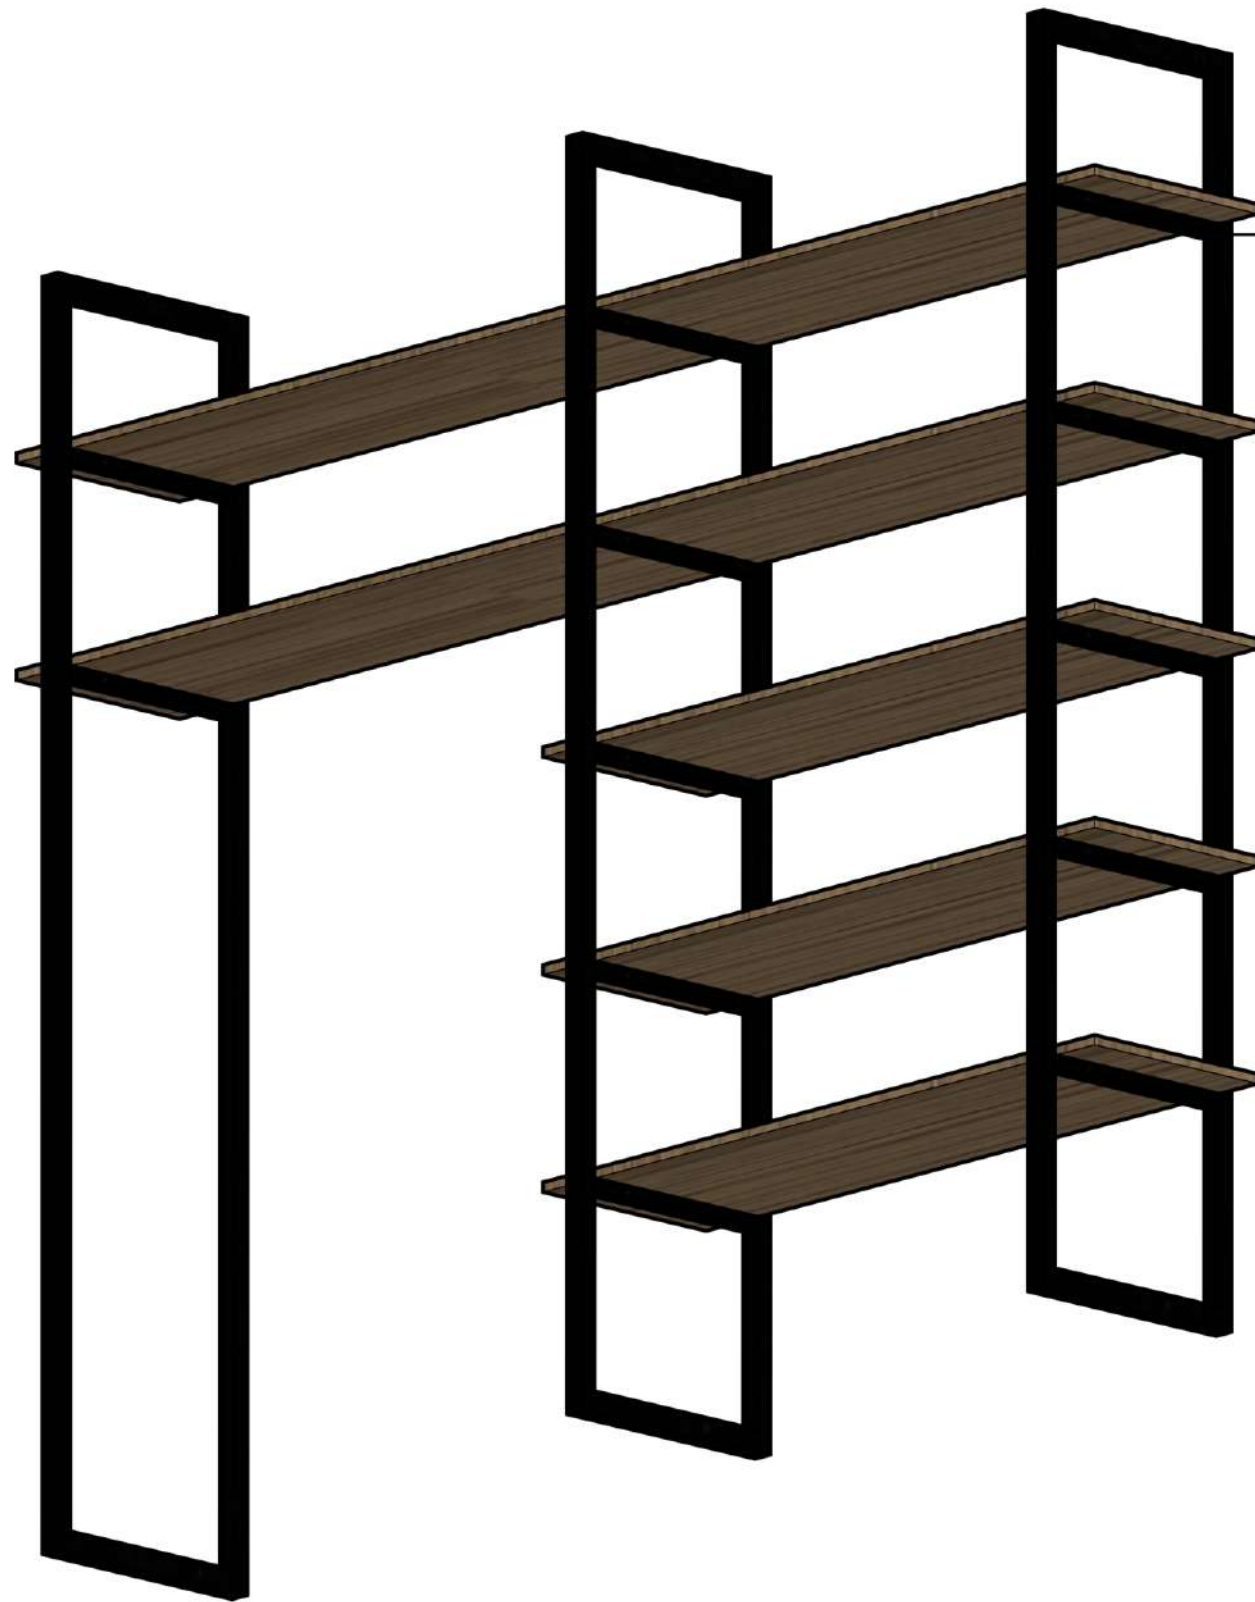

TRAVESAÑO/SOPORTE
DE CAÑO ESTRUCTURAL
DE HIERRO DE 40 X 20 X
1,2 MM

FICHA TÉCNICA

Descripción

Estante autoportante con estructuras de hierro para exhibición y almacenamiento de productos, de diseño industrial abierto que facilita reposición y limpieza. Con espacio cómodo de 1,63 m altura x 1,32 m largo para dos heladeras de exhibición de bebidas.

Medidas generales

Sus dimensiones totales son 2,80 m largo x 0,46 m profundidad x 2,35 m altura

Materiales

Melamina Faplac
Carvalho Mezzo Linea
Nature de 18mm


Caño estructural de
hierro de 40 x 40 x 1,2
mm



Observaciones

Verificar medidas en obra. Sujeto a confirmación final según el carpintero/herrero considere.

MUEBLE BAJO MODULAR

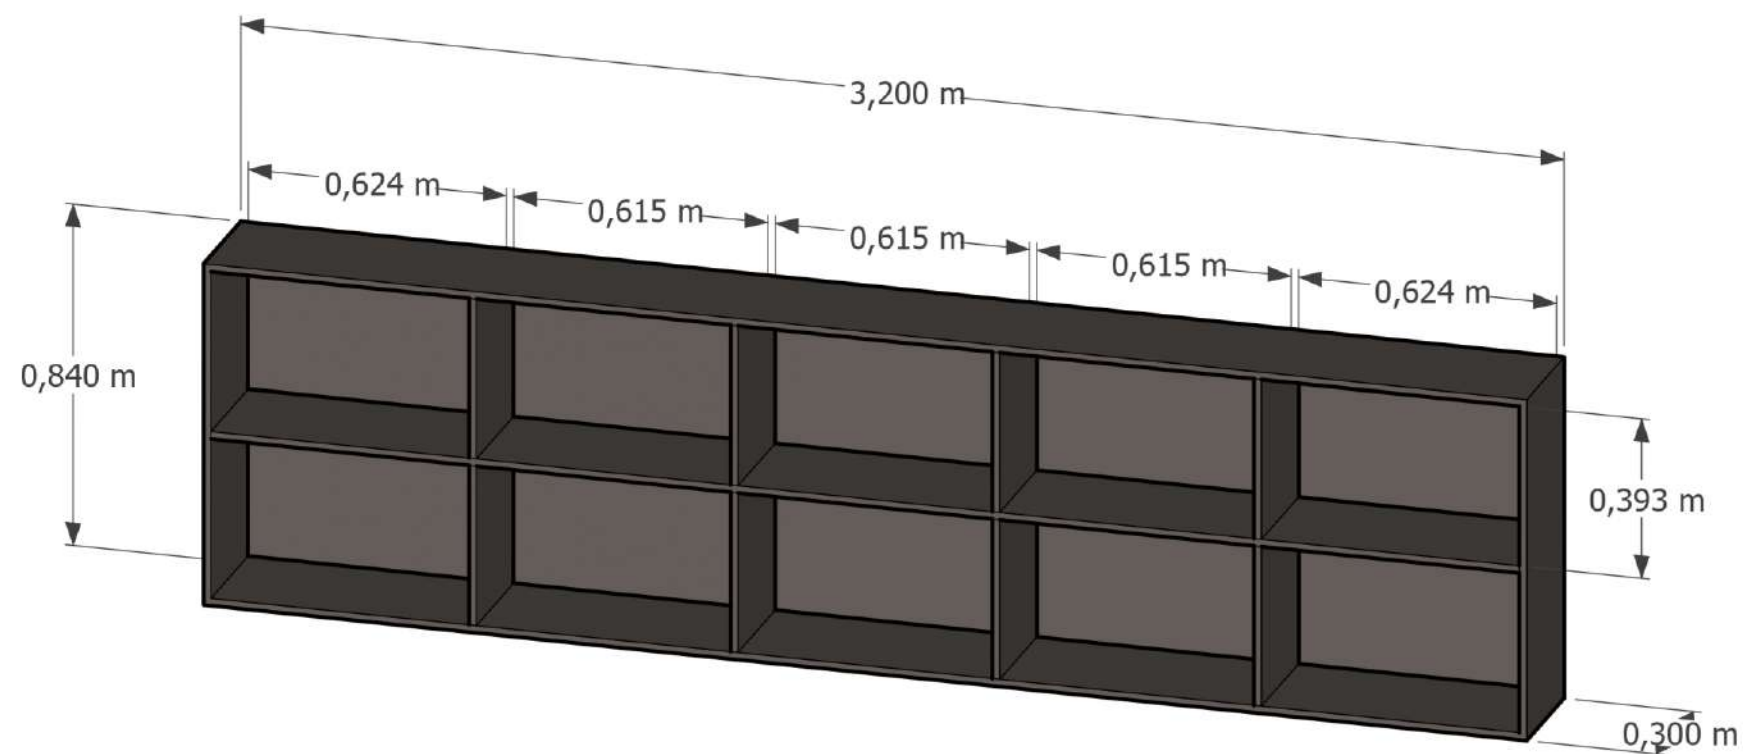

FICHA TÉCNICA

Descripción


Mueble bajo de almacenamiento compuesto por módulos abiertos, apto para guardado y apoyo en el área comercial. Ubicado detrás del mostrador. Diseño compacto y funcional.

Medidas generales

Sus dimensiones totales son 3,20 m largo x 0,30 m profundidad x 0,84 m altura

Materiales


Melamina Faplac Tribal Linea Étnica de 18mm

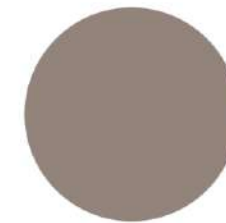

Observaciones

Verificar medidas en obra. Sujeto a confirmación final según el carpintero considere.

MUEBLE BAJO MODULAR

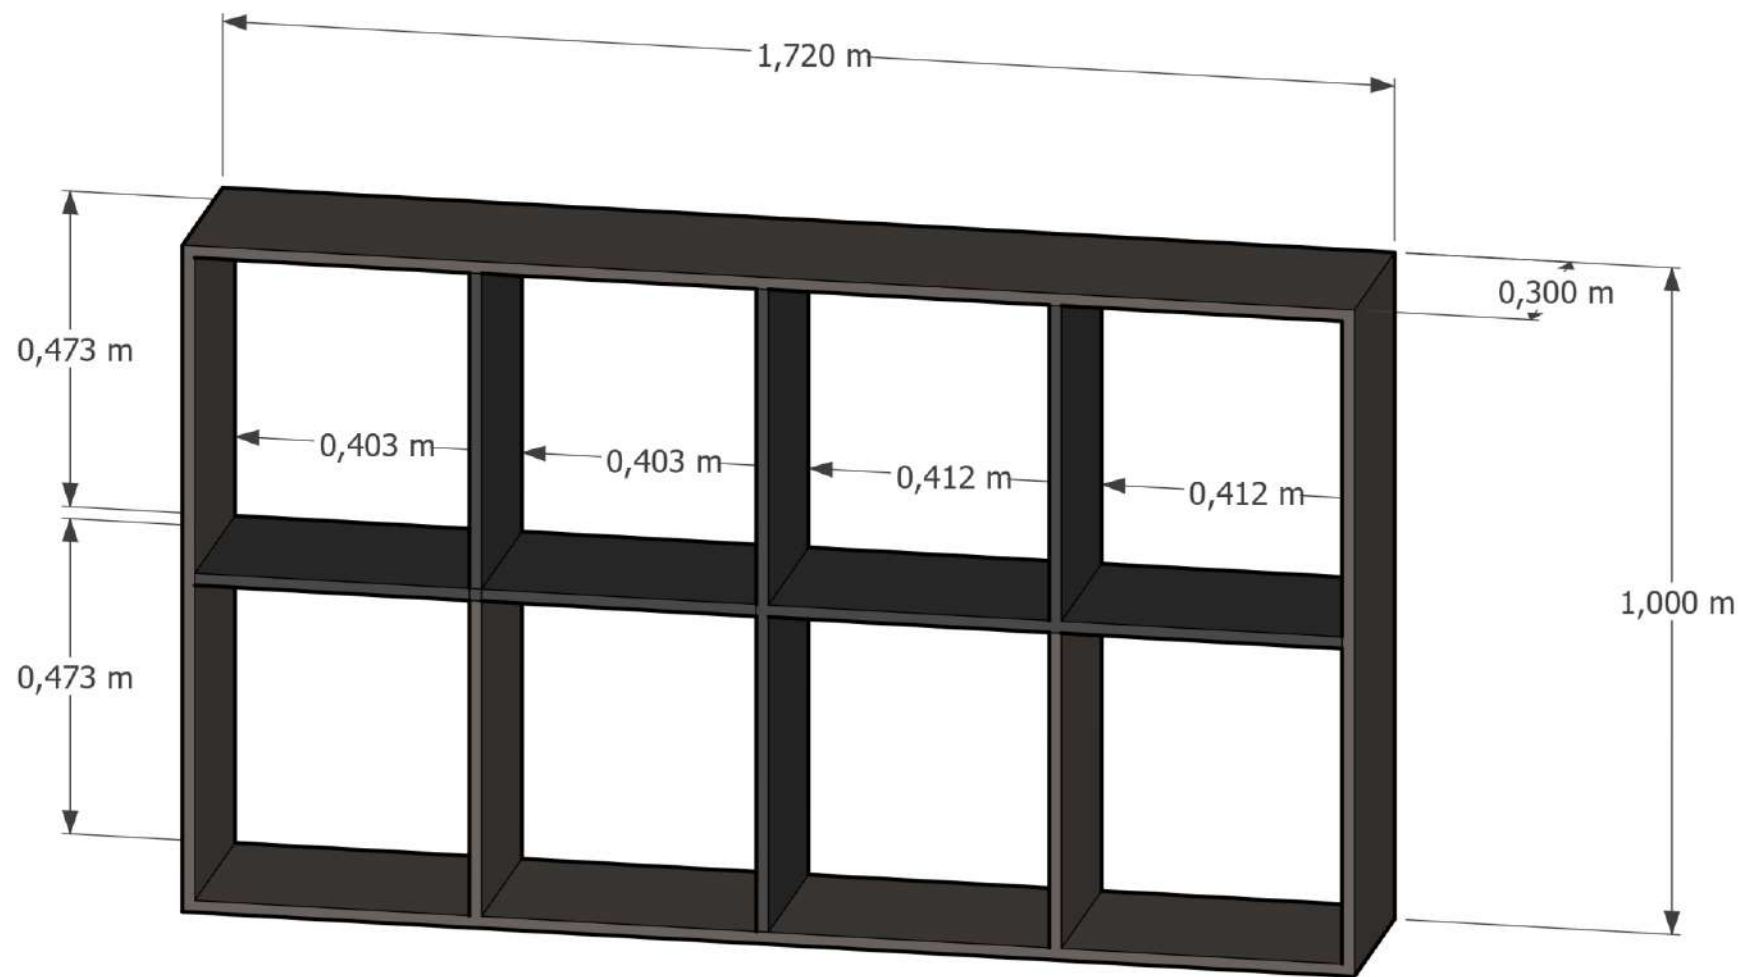

FICHA TÉCNICA

Descripción


Mueble bajo de almacenamiento compuesto por módulos abiertos, apto para guardado y apoyo en el área comercial. Ubicado debajo de la ventana del comercio, para mayor comodidad en atención a clientes.

Medidas generales

Sus dimensiones totales son 1,72 m largo x 0,30 m profundidad x 1,00 m altura

Materiales

Melamina Faplac Tribal Línea Étnica de 18mm

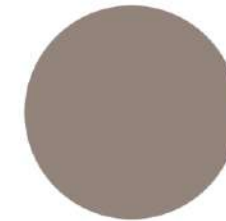

Observaciones

Verificar medidas en obra. Sujeto a confirmación final según el carpintero considere.

ESTANTERÍA



FICHA TÉCNICA

Descripción


Mueble de exhibición vertical de productos que facilita la reposición de los mismos y visualización. Superficie resistente al uso comercial.

Medidas generales

Sus dimensiones totales son 1,40 m largo x 0,30 m profundidad x 2,00 m altura

Materiales

Melamina Faplac Tribal Linea Étnica de 18mm

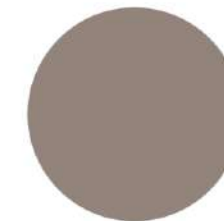


Observaciones

Verificar medidas en obra. Sujeto a confirmación final según el carpintero considere.

La cartelería frontal en los estantes es referencial y se encuentra sujeta a modificación según criterios comerciales o preferencias del cliente.

MUEBLE ESQUINERO

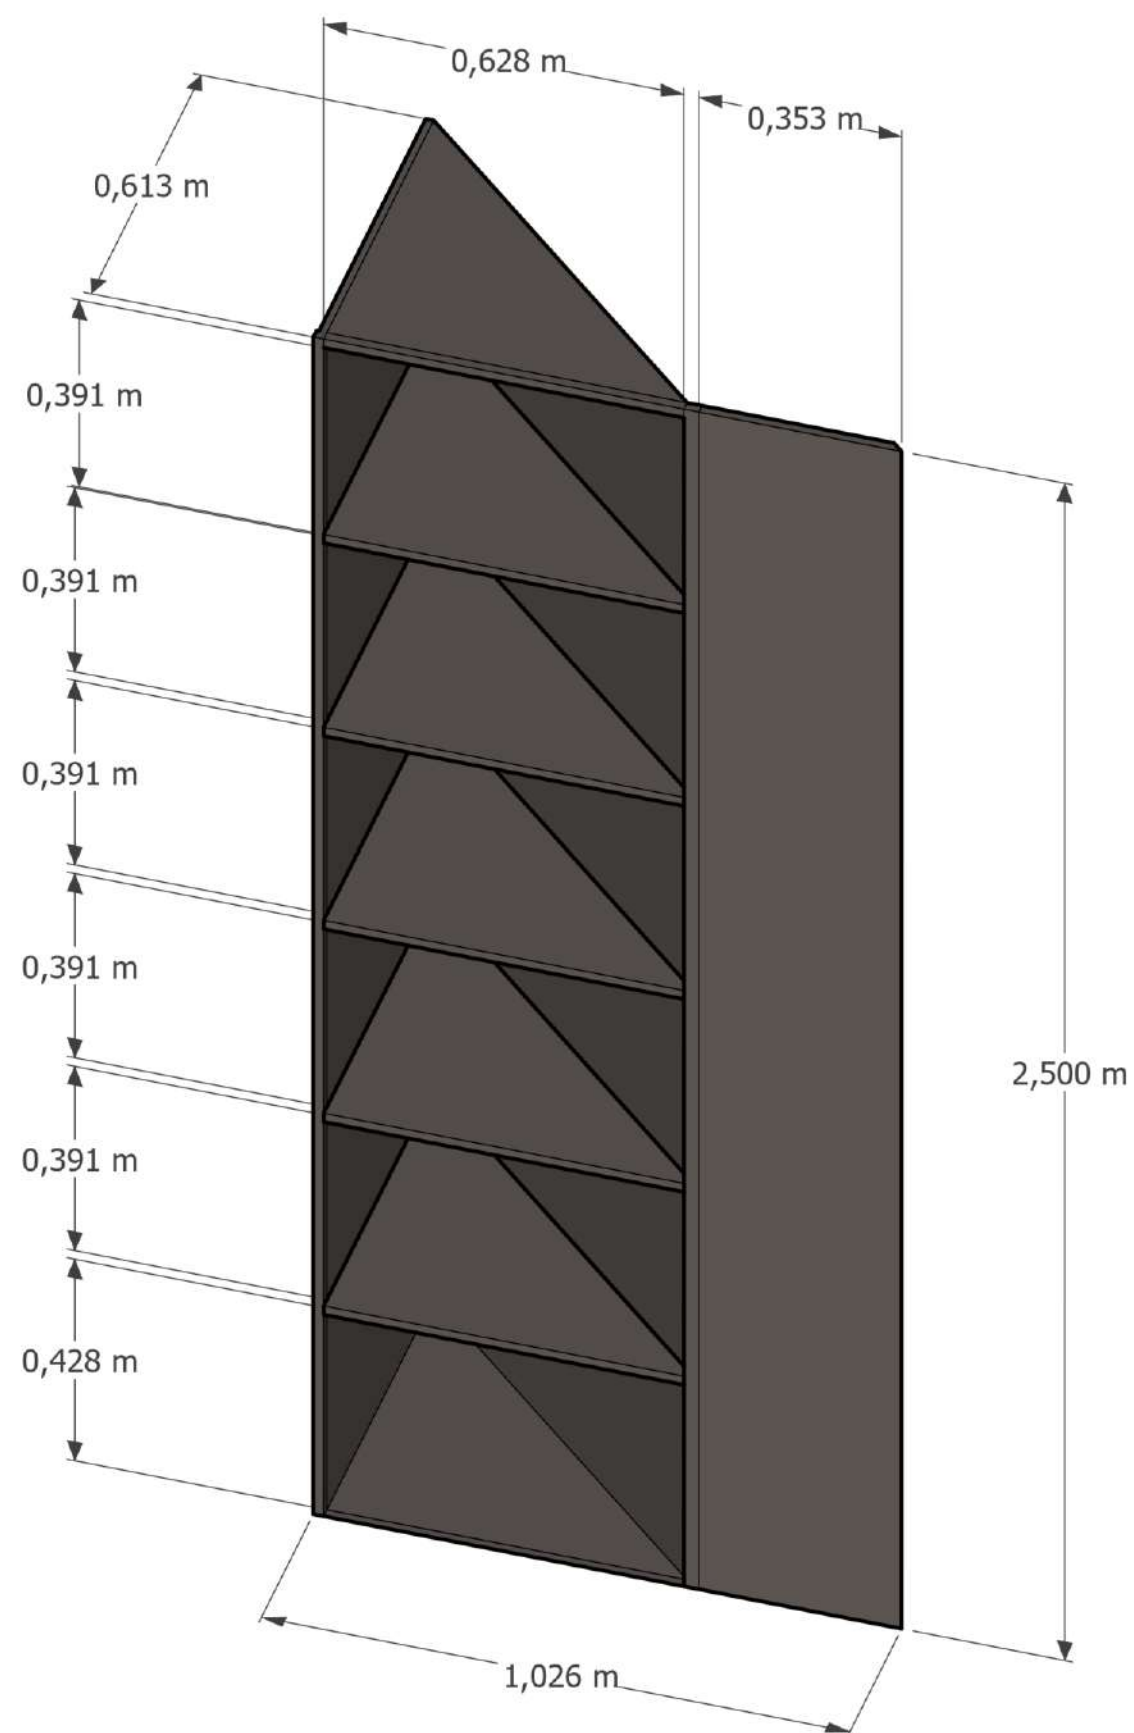

FICHA TÉCNICA

Descripción

Mueble destinado a la exhibición de productos, diseñado para optimizar espacio en esquina condicionado por instalaciones técnicas existentes.

Medidas generales

Sus dimensiones totales son 1,02 m largo x 0,61 m profundidad x 2,50 m altura

Materiales


Melamina Faplac Tribal Línea Étnica de 18mm



Observaciones

Verificar medidas en obra. Sujeto a confirmación final según el carpintero considere.

REVESTIMIENTO

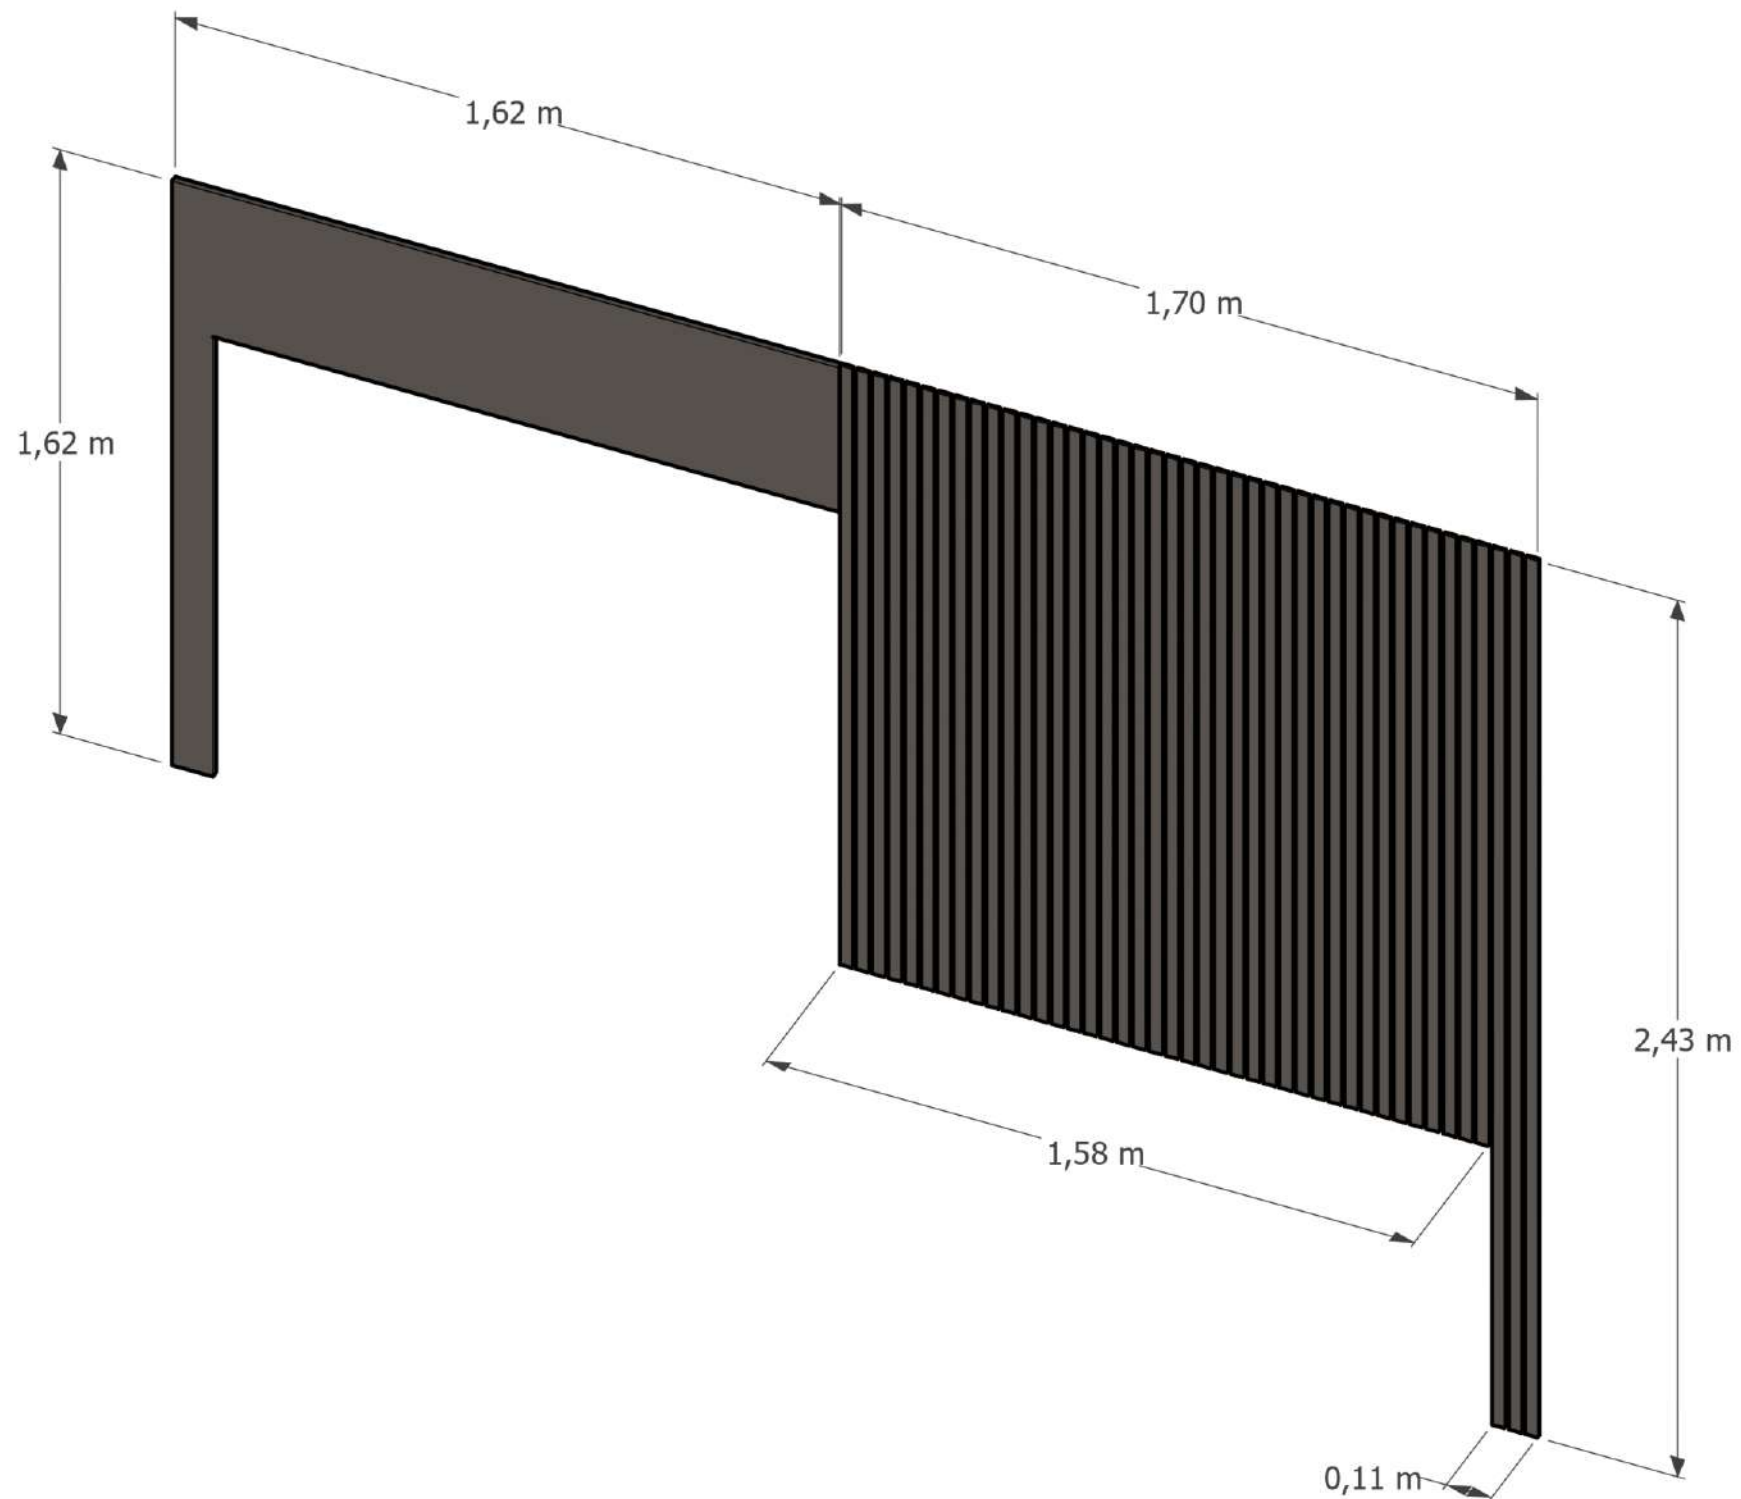

FICHA TÉCNICA

Descripción

Panel de WPC simulando un revestimiento varillado de madera. Ubicado detrás del mostrador. Función exclusivamente estética aportando textura y calidez al espacio. Revestimiento para ventana interior del local.


Medidas generales

Dimensiones totales del panel son 1,70 m largo x 2,43 m altura. Tiene un espesor de 13,5 mm. Dimensión total del revestimiento para ventana es de 1,62 m largo x 1,62 m alto.

Materiales

Melamina Faplac Tribal
Linea Étnica de 18mm

Panel de WPC Wud
Linea Nikko Grey

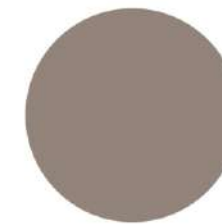


Observaciones

Verificar medidas en obra. Sujeto a confirmación final según el carpintero considere.

06 CARPINTERÍA Y HERRERÍA

ABERTURAS - PUERTA GRANERO

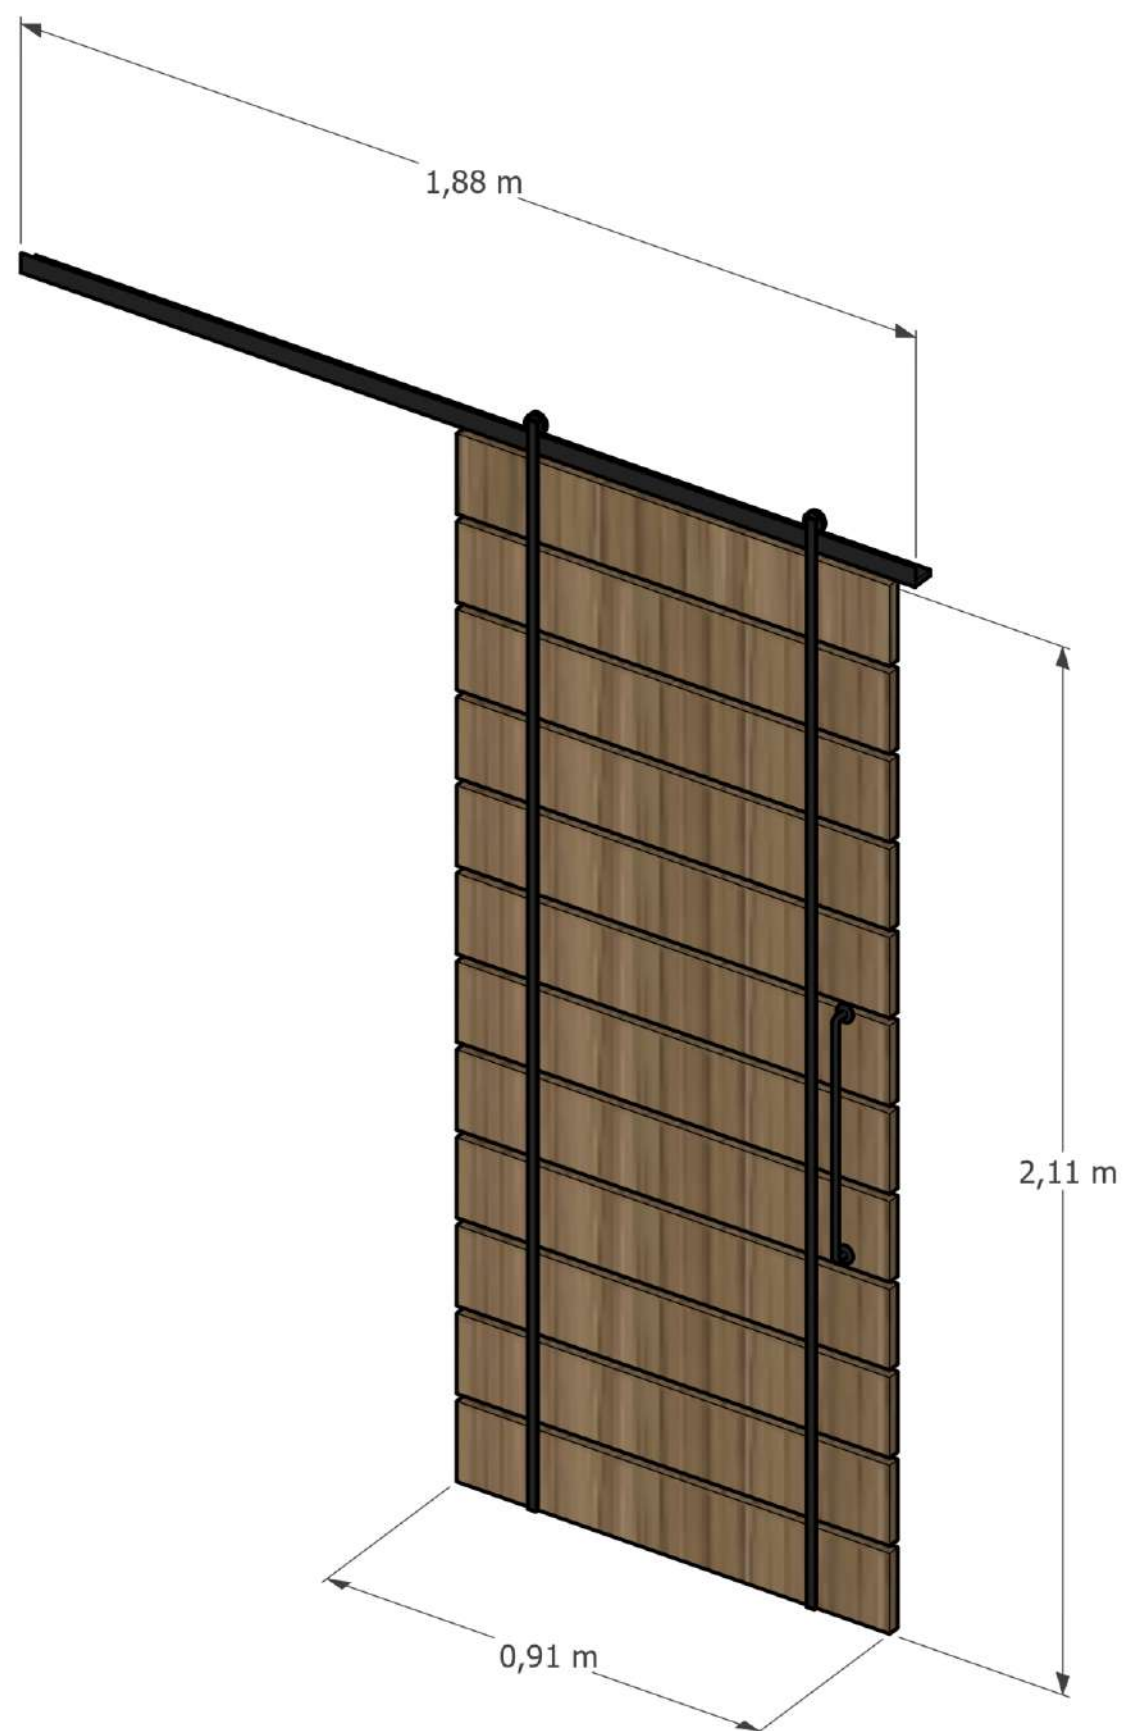

FICHA TÉCNICA

Descripción

Puerta corrediza tipo granero, de una hoja mediante sistema de riel superior visto. El diseño aporta carácter estético al espacio, permitiendo el cierre de un ambiente sin interferir con el uso de espacio interior, permitiendo buena circulación

Medidas generales

Sus dimensiones totales son 1,88 m largo x 2,11 m altura .

Materiales

Melamina Faplac
Carvalho Mezzo Linea
Nature de 18mm


Sistema de riel y
manija de hierro



Observaciones

Verificar medidas en obra. Sujeto a confirmación final según el carpintero considere.

ABERTURAS - HERRERÍA

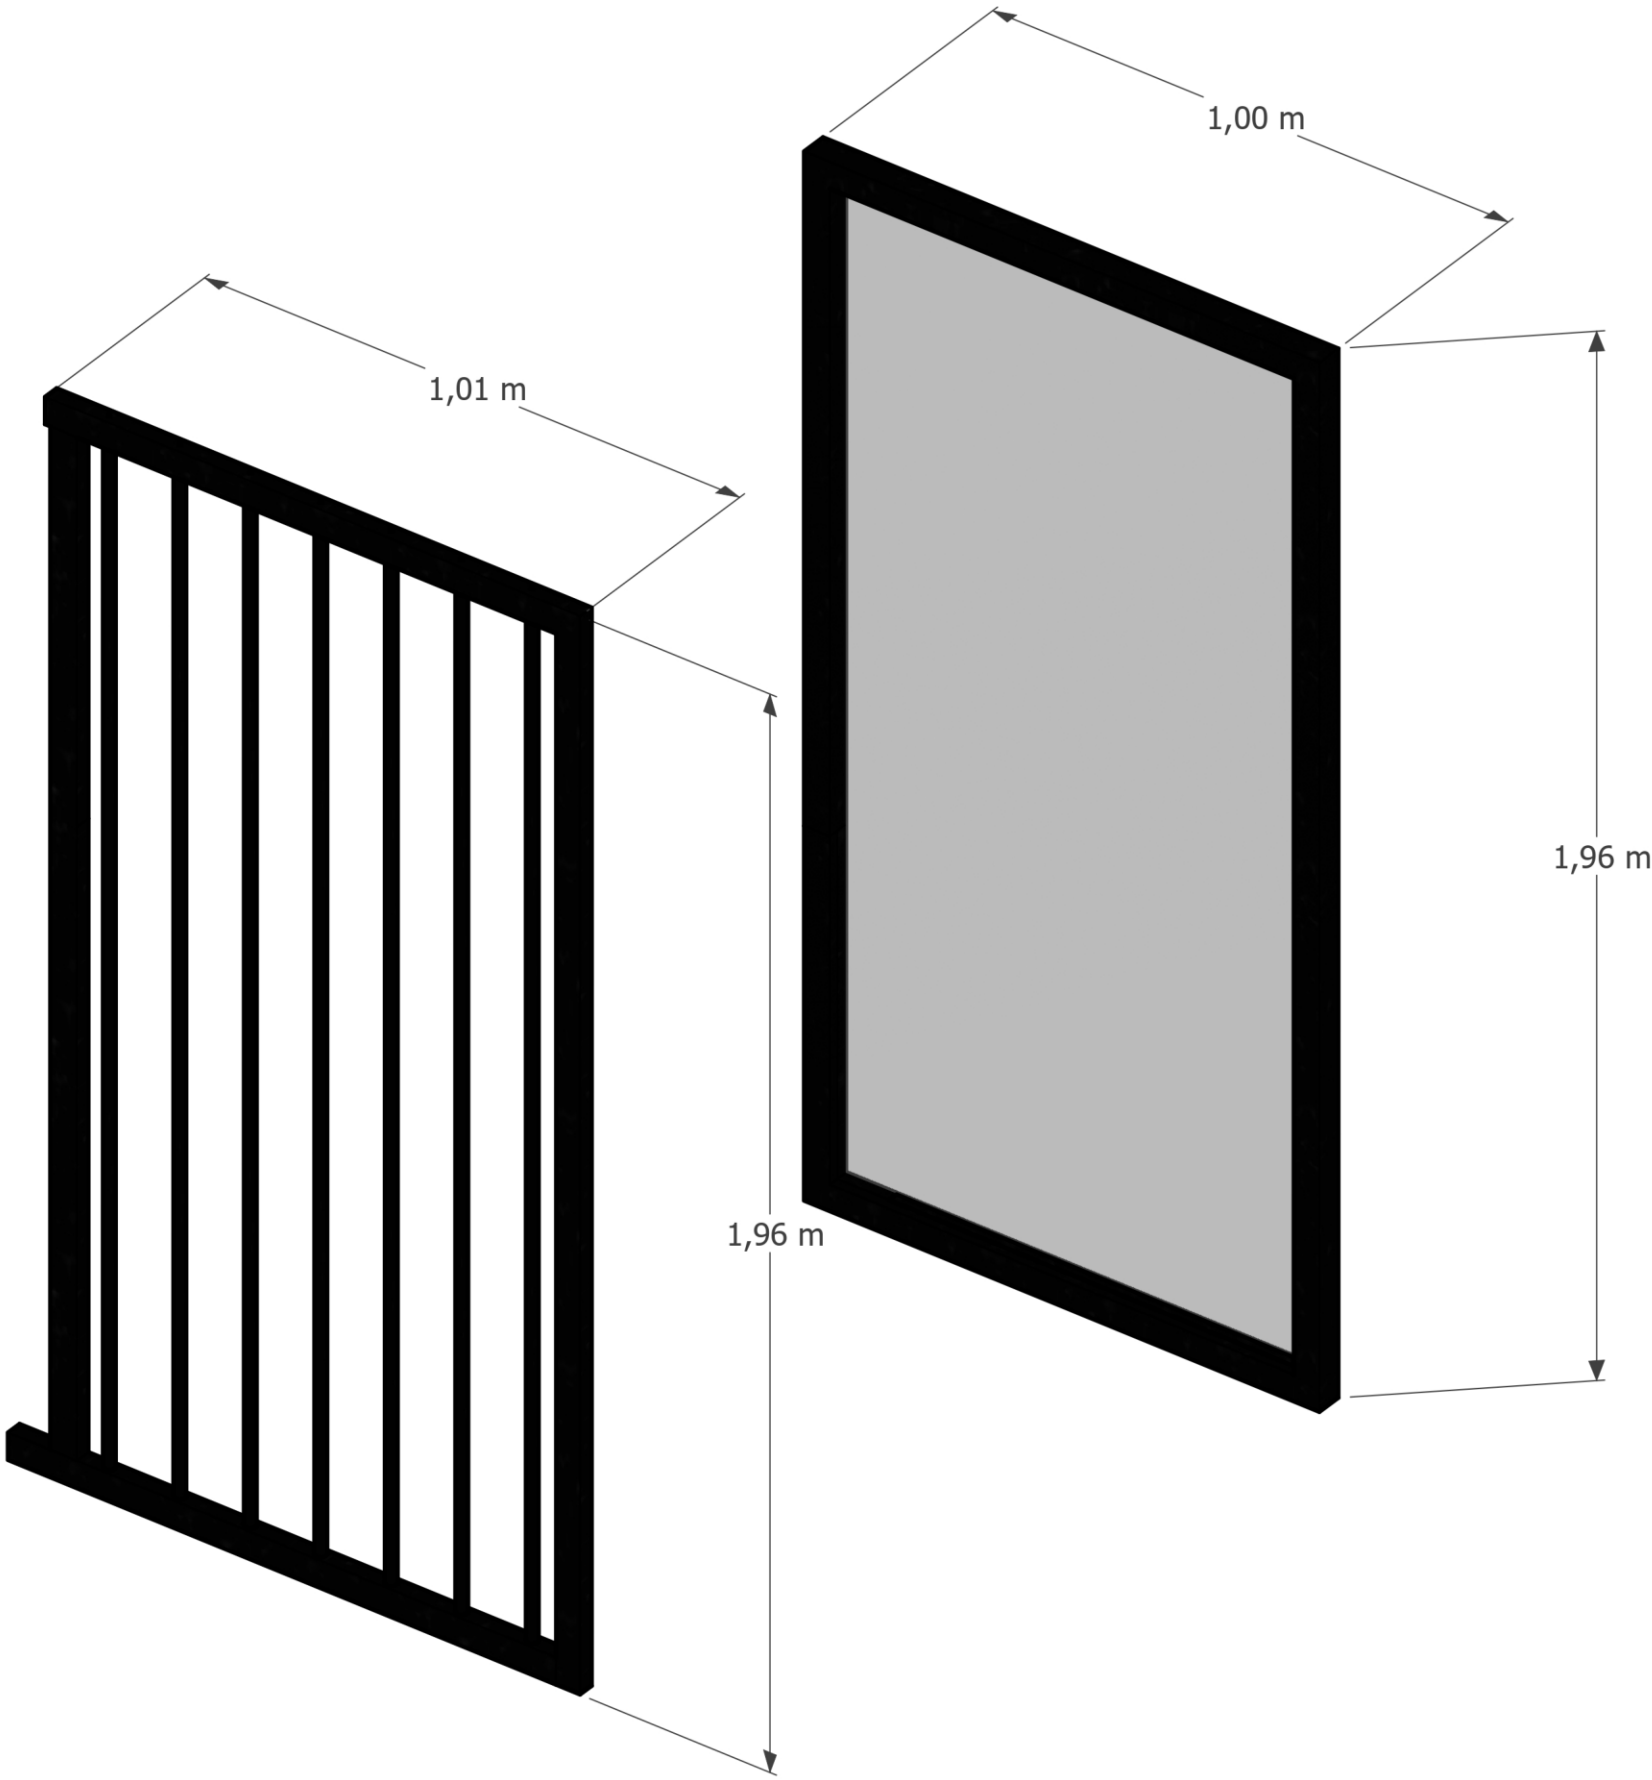

FICHA TÉCNICA

Descripción


Puerta principal de entrada al local de estructura metálica con vidrio de seguridad laminado enrejada con separaciones de 12 cm entre tubos. Diseño en función a la seguridad del local y cliente.

Medidas generales

Sus dimensiones totales son 1,88 m largo x 2,11 m altura .
Tiene una apertura de 180°.

Materiales


Caños cuadrado estructural de 40 x 40 x 1.6 mm y caño redondo de Ø 40 x 1,6 mm

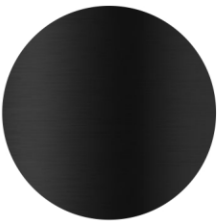

Observaciones

Verificar medidas en obra. Sujeto a confirmación final según el herrero considere.

ABERTURAS - HERRERÍA

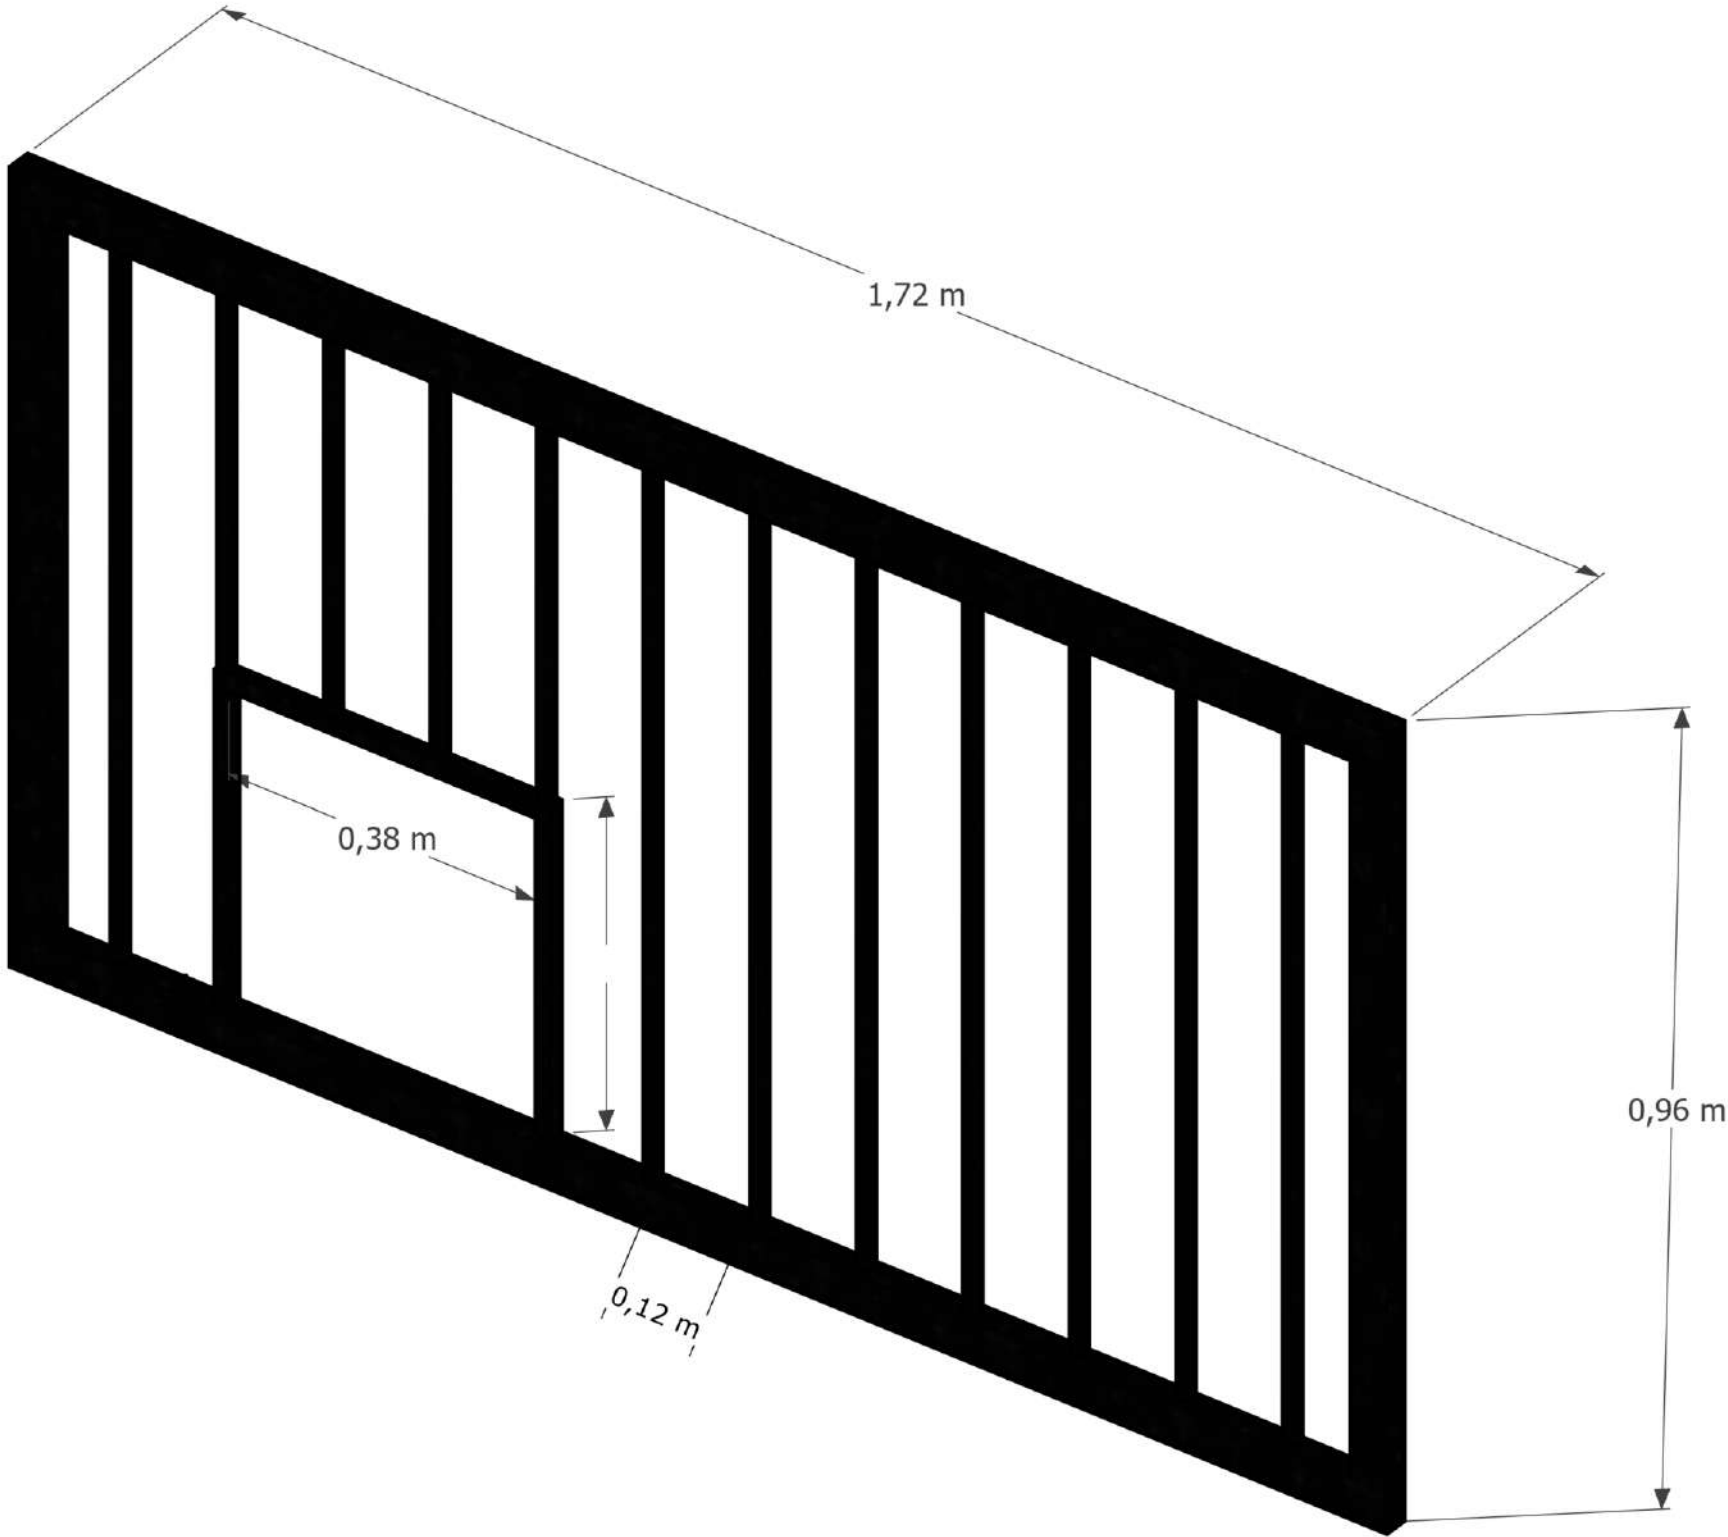

FICHA TÉCNICA

Descripción
Ventana principal de entrada al local de estructura metálica con vidrio de seguridad laminado enrejada con separaciones de 12 cm entre tubos. Diseño en función a la seguridad del local y cliente aportando una abertura de 38 m x 40 m para comodidad de alcance de productos a los clientes.


Medidas generales
Sus dimensiones totales son 1,72 m largo x 0,96 m altura .

Materiales
Caños cuadrado estructural de 40 x 40 x 1.6 mm y caño redondo de Ø 40 x 1,6 mm



Observaciones
Verificar medidas en obra. Sujeto a confirmación final según el herrero considere.

ABERTURAS - HERRERÍA

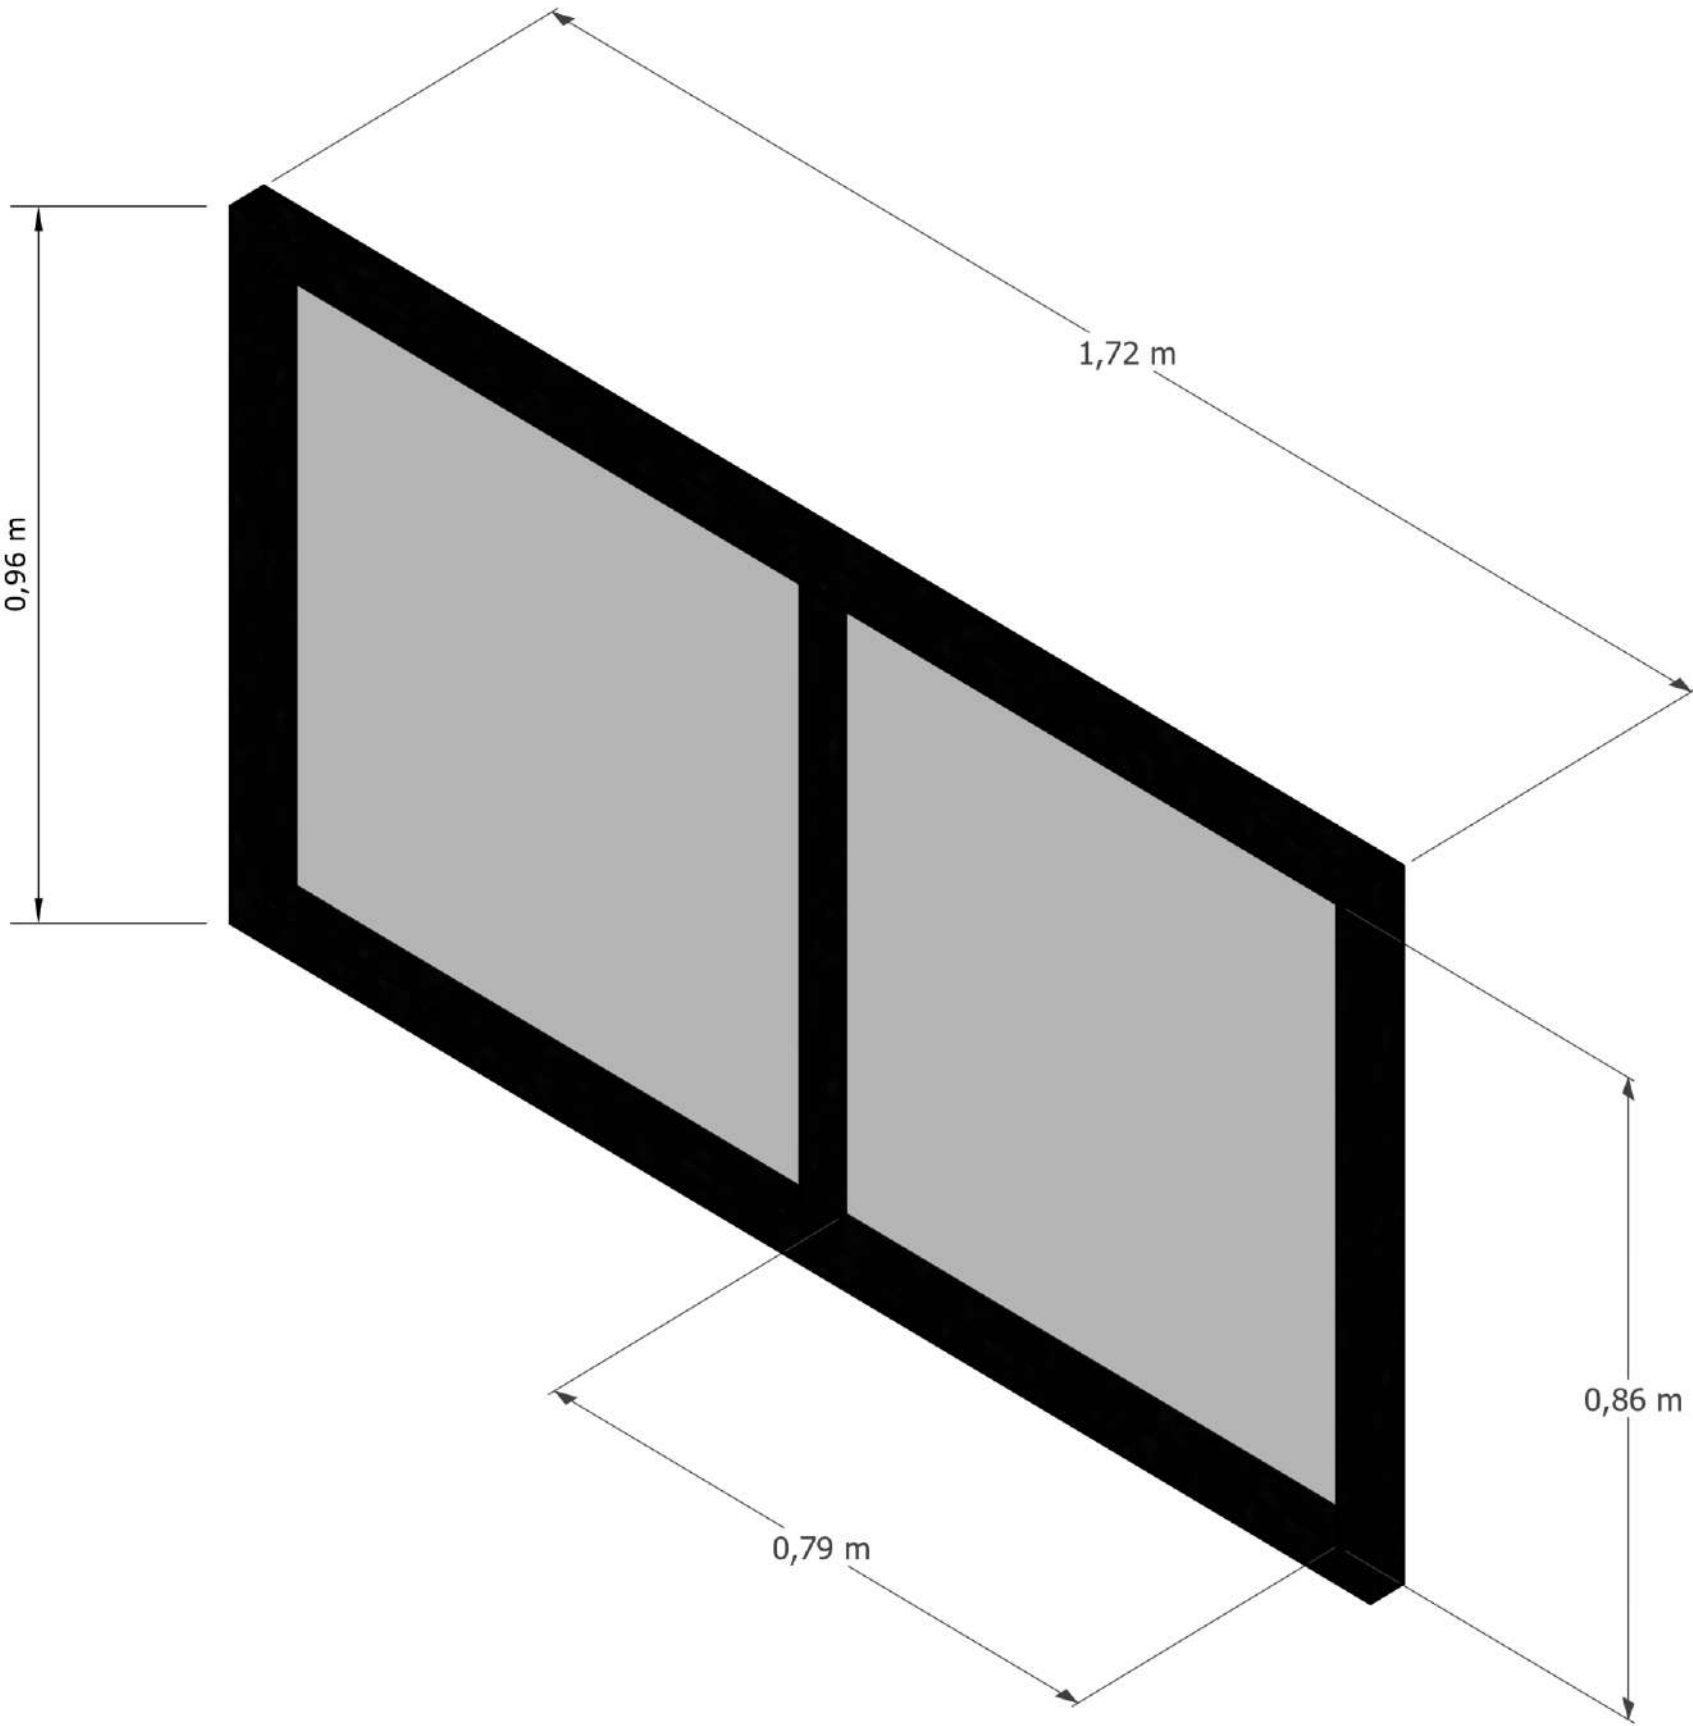

FICHA TÉCNICA


Descripción
Ventana corrediza de dos hojas con vidrio laminado de seguridad. Carpintería de hierro estructural.

Medidas generales
Sus dimensiones totales son 1,72 m largo x 0,96 m altura .

Materiales
Caños cuadrado estructural de 40 x 40 x 1.6 mm



Observaciones
Verificar medidas en obra. Sujeto a confirmación final según el herrero considere.

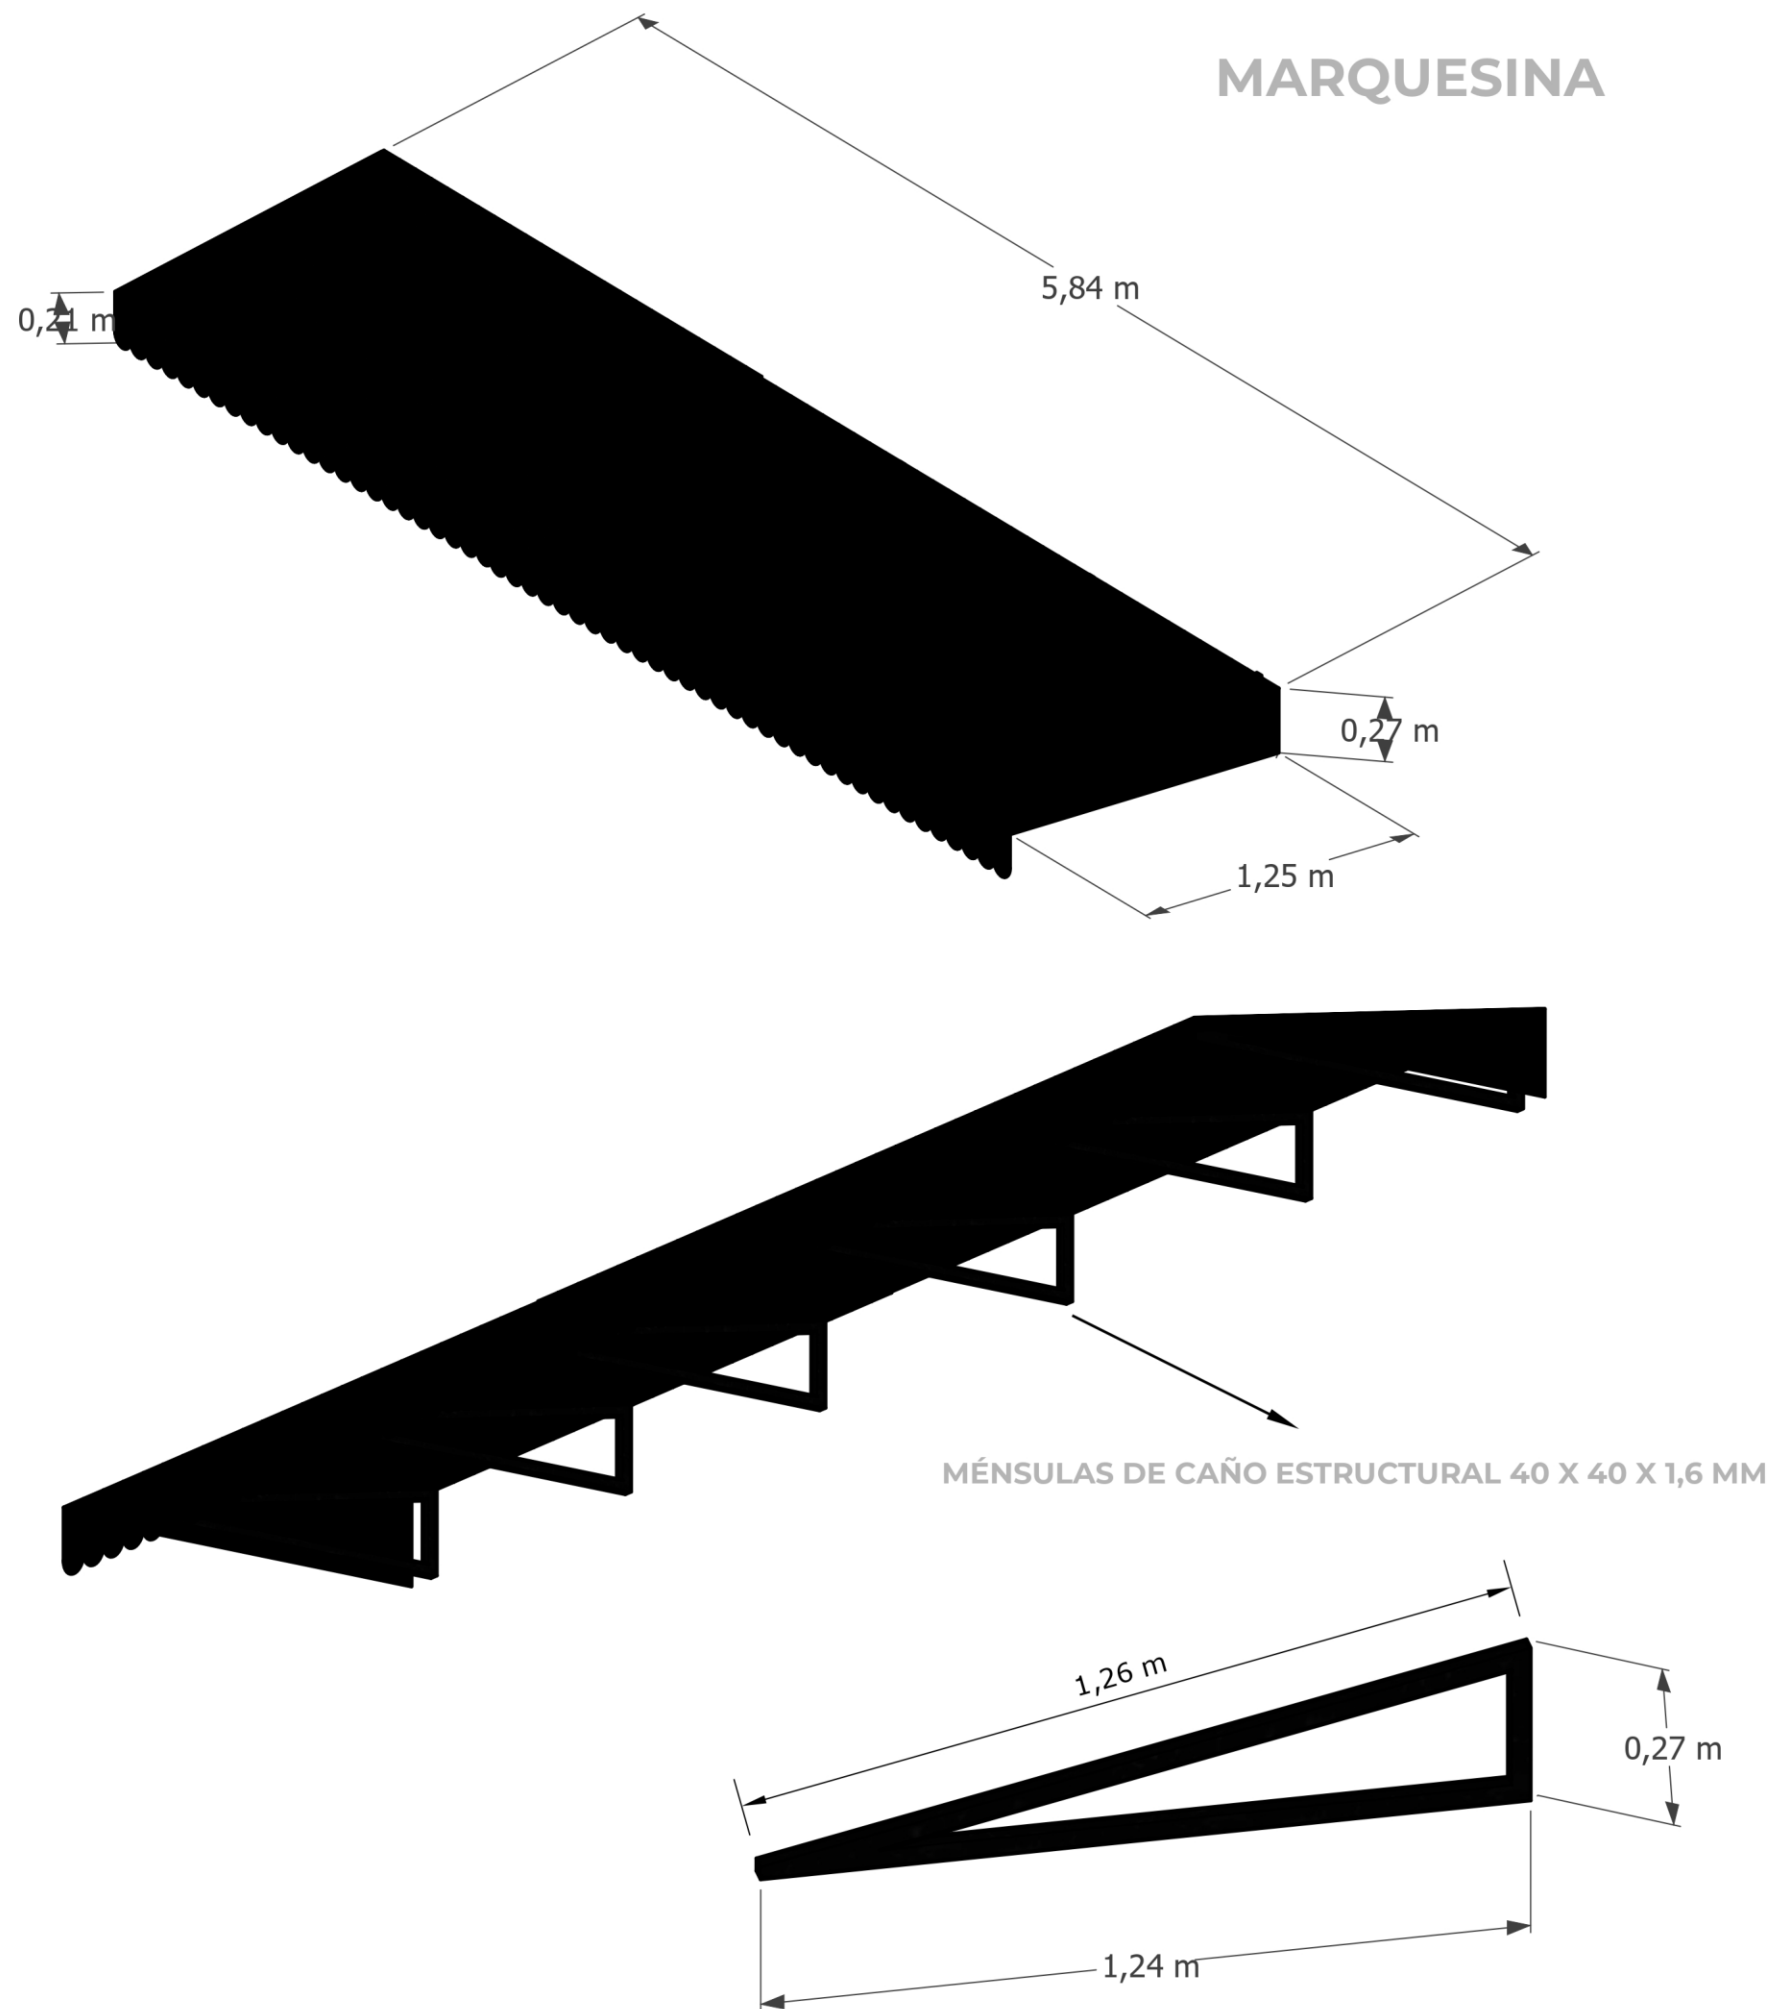

FICHA TÉCNICA

Descripción


Marquesina ubicada sobre el acceso del local de chapa galvanizada lisa sobre mensulas semiocultas ancladas a fachada. La elección de la chapa galvanizada le da un aspecto mas fino y arquitectónico a la fachada. Su diseño aparte de ser estético, cumple una función de protección climática.

Medidas generales

Sus dimensiones totales son 5,84 m largo x 1,25 m profundidad x 0,47 altura.

Materiales

Caños cuadrado estructural de 40 x 40 x 1.6 mm
Chapa galvanizada lisa calibre 18 / 20 de espesor

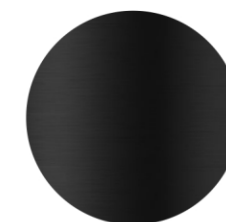

Observaciones

Verificar medidas en obra. Sujeto a confirmación final según el herrero considere.

07 IDENTIDAD VISUAL

IDENTIDAD VISUAL

Logo



Isologo




Tipografía


Principal: Sochelia
Aa Bb Cc Dd Ee Ff Gg Hh Ii Jj Kk Ll Mm Nn Nn Oo Pp Qq Rr Ss Tt Uu Vv Ww Xx Yy Zz
0123456789 !"#%&/()=?

Secundaria: Caviar Dreams
Aa Bb Cc Dd Ee Ff Gg Hh Ii Jj Kk Ll Mm Nn Ññ Oo Pp Qq Rr Ss Tt Uu Vv Ww Xx Yy Zz
0123456789 !"#%&/()=?i


Paleta de colores

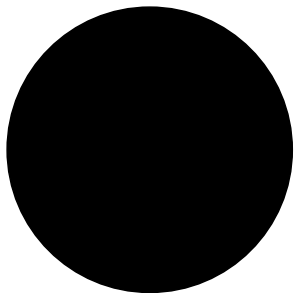


#201E1E
RGB 32 30 30
CMYK 100 100 100 100

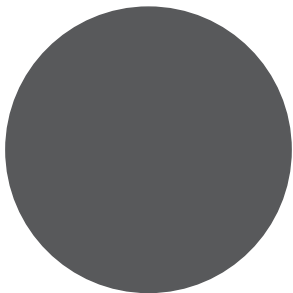


#606062
RGB 96 96 98
CMYK 0 0 0 82

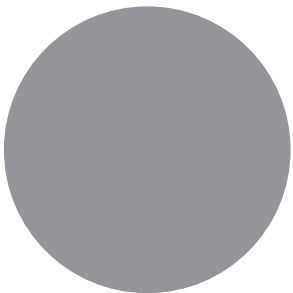

#96989A
RGB 150 152 154
CMYK 0 0 0 50

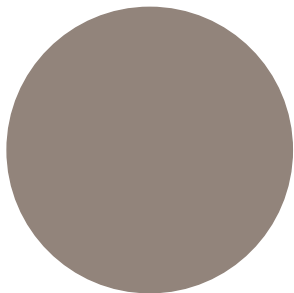

#92847B
RGB 146 132 123
CMYK 0 0 0 82

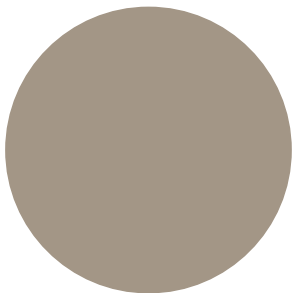

#A39686
RGB 163 150 134
CMYK 38 38 48 3



#F1F1F2
RGB 241 241 242
CMYK 0 0 0 5

Combinaciones



APLICACIONES

Cartelería



Packaging



08 PLANIMETRÍA DE CARTELERÍA - SEÑALÉTICA

UBICACIÓN DE CARTELERÍA

Carteles indicativos

Rectángulos de PVC
impreso en estanterías

Carteles indicativos

Rectángulos de PVC
impreso en estanterías

Cartel principal

Cenefa de chapa acanalada
enmarcada pintada de color negro

Letras corpóreas de chapa
retroiluminadas pintadas de blanco
con iluminación cálida.

Cartel secundario

Logo de polyfan de 2 cm
pintado de color blanco

Cartel colgante

Rectángulo de pvc impreso
colgado a cielorraso

Carteles indicativos

Rectángulos de PVC
impreso en estanterías

Carteles indicativos

Rectángulos de PVC
impreso en estanterías


Vinilo de corte

Vinilo de corte en
mueble esquinero


CARTELERIA EXTERIOR

1) Cartel principal

Cenefa de chapa acanalada enmarcada pintada de color negro

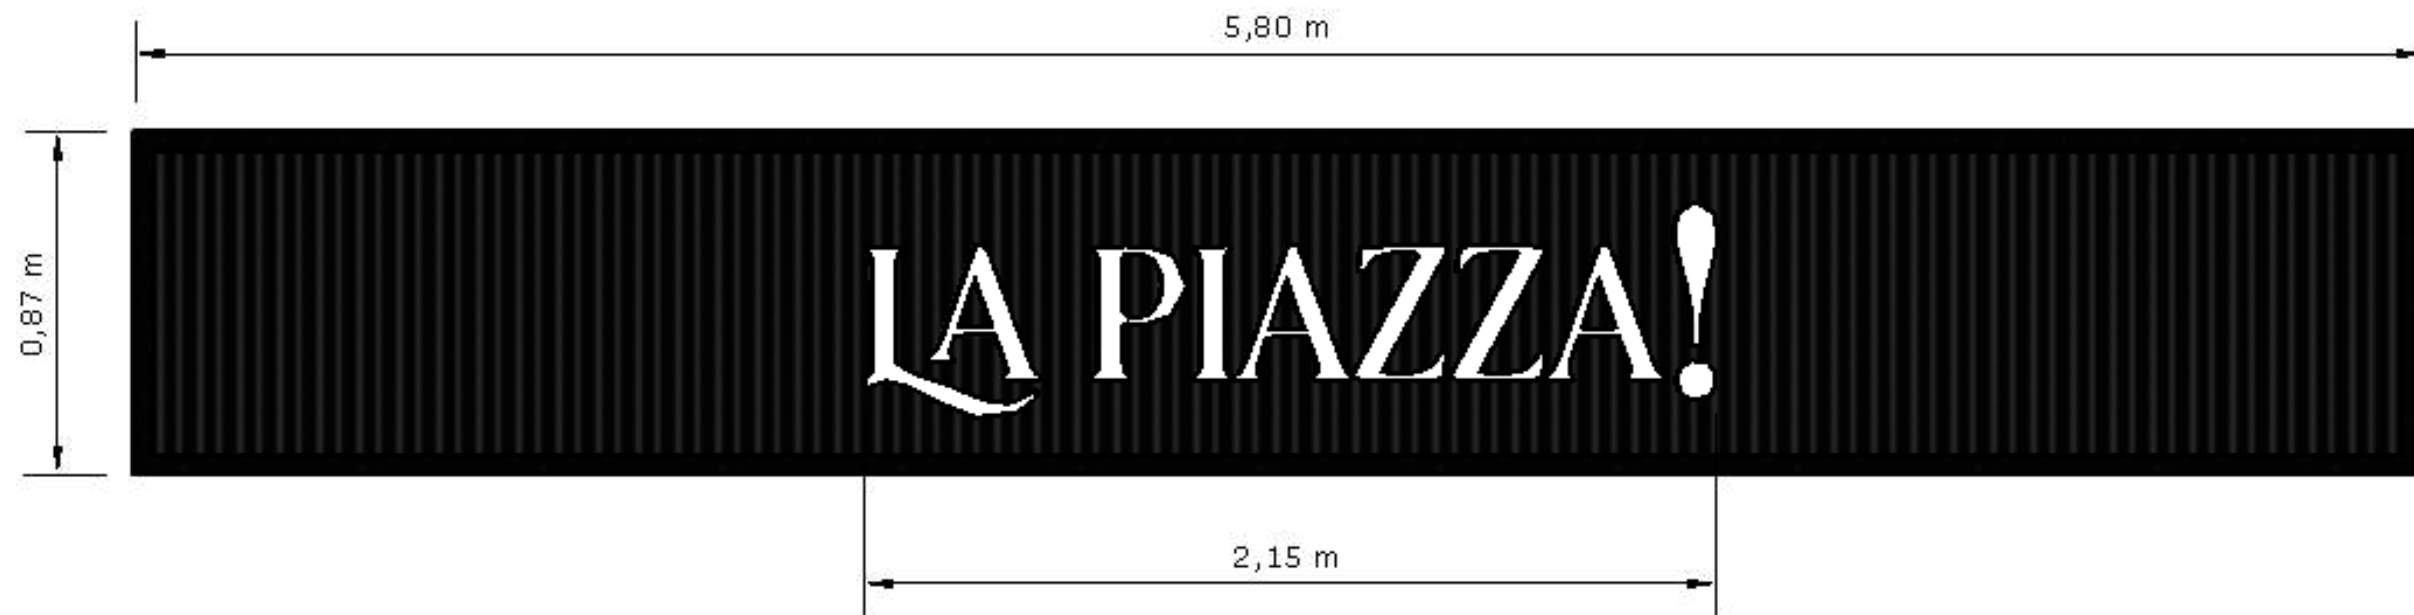

Letras corpóreas de chapa retroiluminadas pintadas de blanco con iluminación cálida.

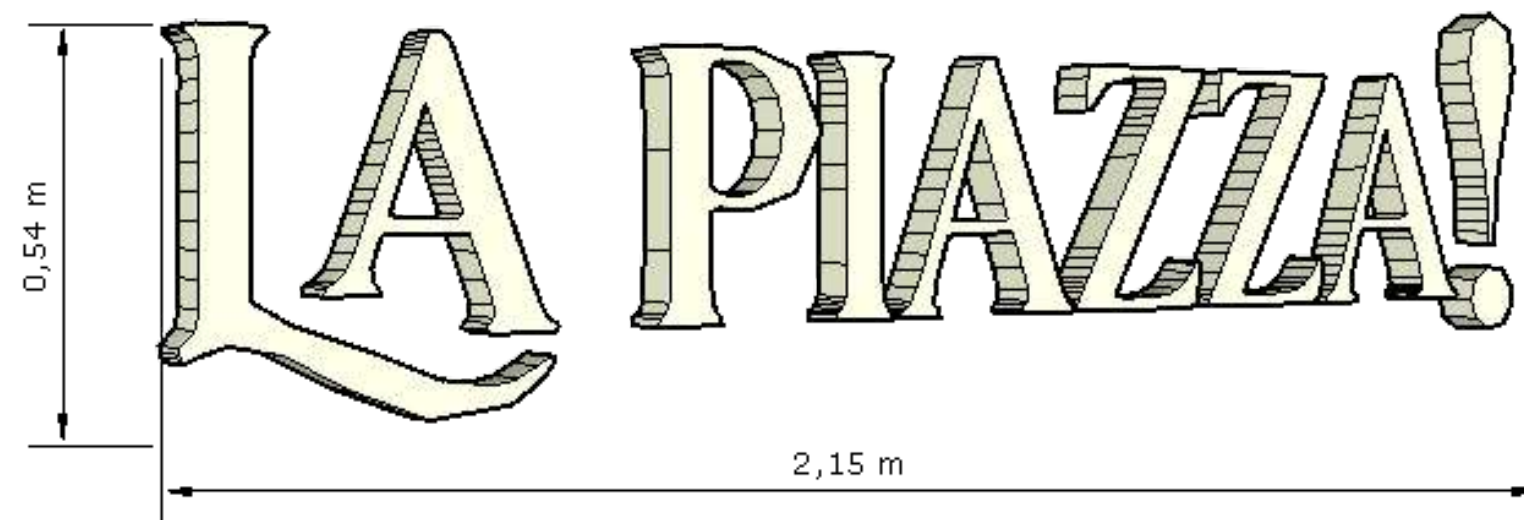


Aclaración: rectificar medidas en obra.

CARTELERIA INTERIOR

1) Cartel secundario


Logo de polyfan de 2 cm pintado de color blanco

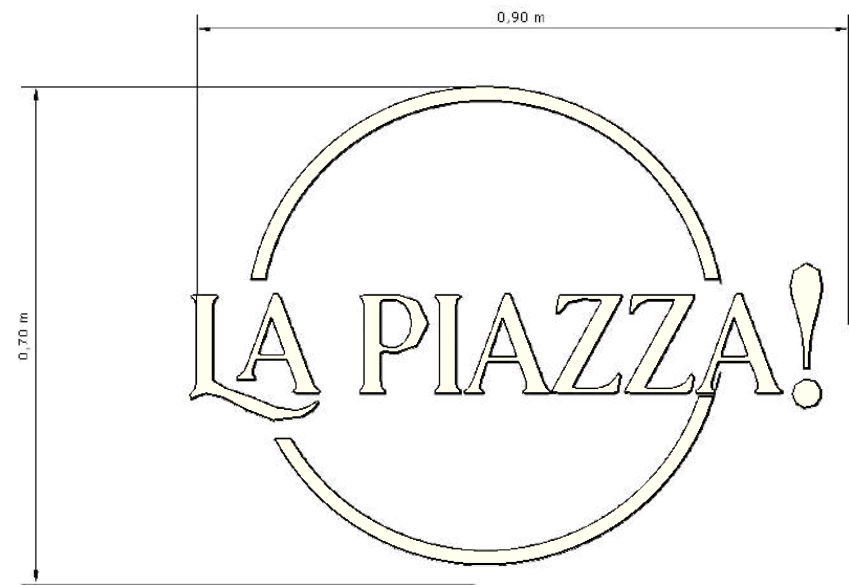

cantidad: 1

2) Cartel colgante


Rectángulo de pvc impreso colgado a cielorraso

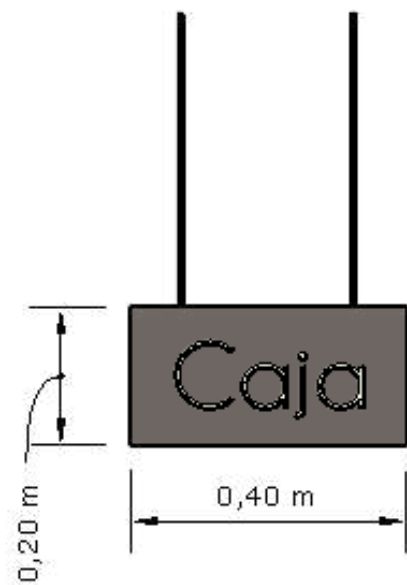

cantidad: 1

3) Carteles indicativos

Rectángulos de PVC impreso en estanterías

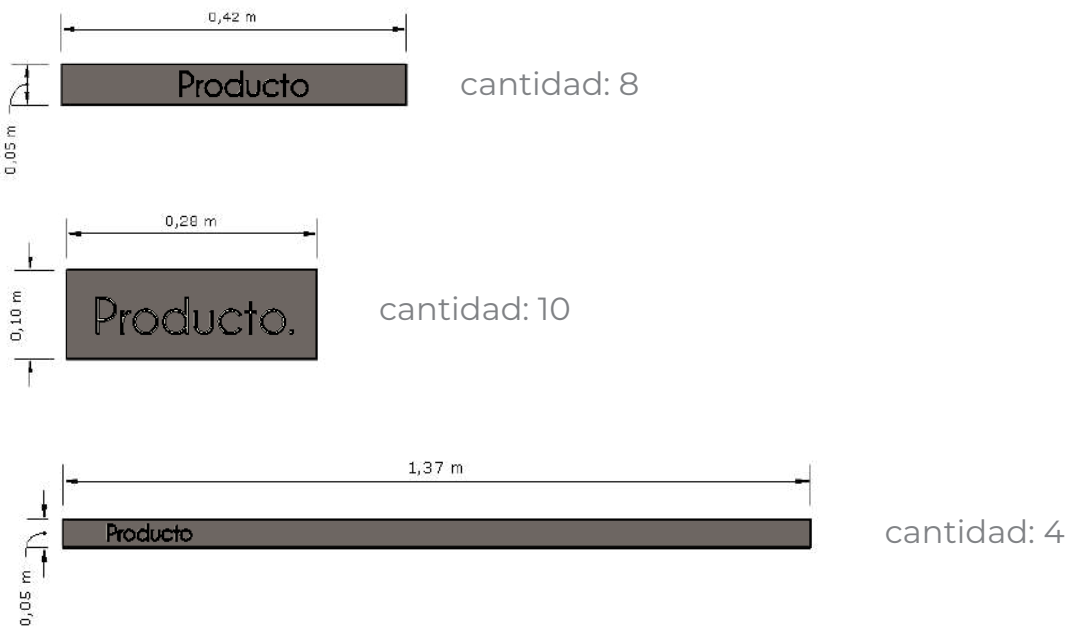

4) Vinilo

Vinilo de corte en mueble esquinero



cantidad: 1

Aclaración: rectificar medidas en obra.

IMAGENES ILUSTRATIVAS

Cartelería exterior



cartel principal

IMAGENES ILUSTRATIVAS

Cartelería interior




cartel secundario



carteles indicativos



carteles indicativos

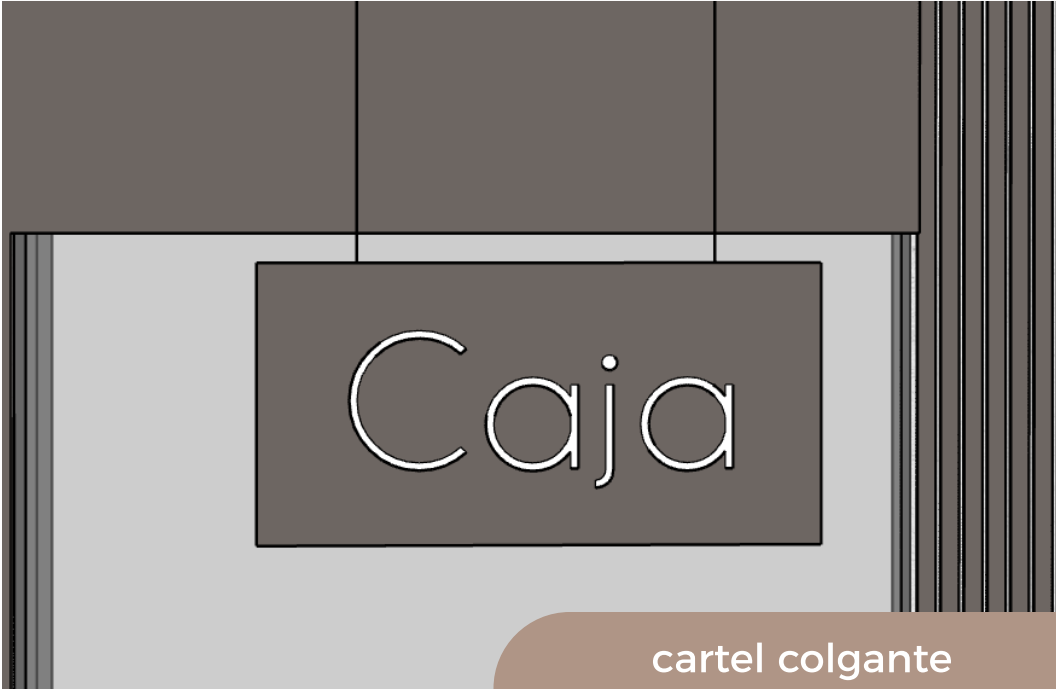

cartel colgante



carteles indicativos



carteles indicativos

09 RENDERS

LA PIAZZA!



Caja

LA PIAZZA!







Caja

LA PIAZZA

arthea.
S T U D I O D E S I G N

@estudio.arthea